


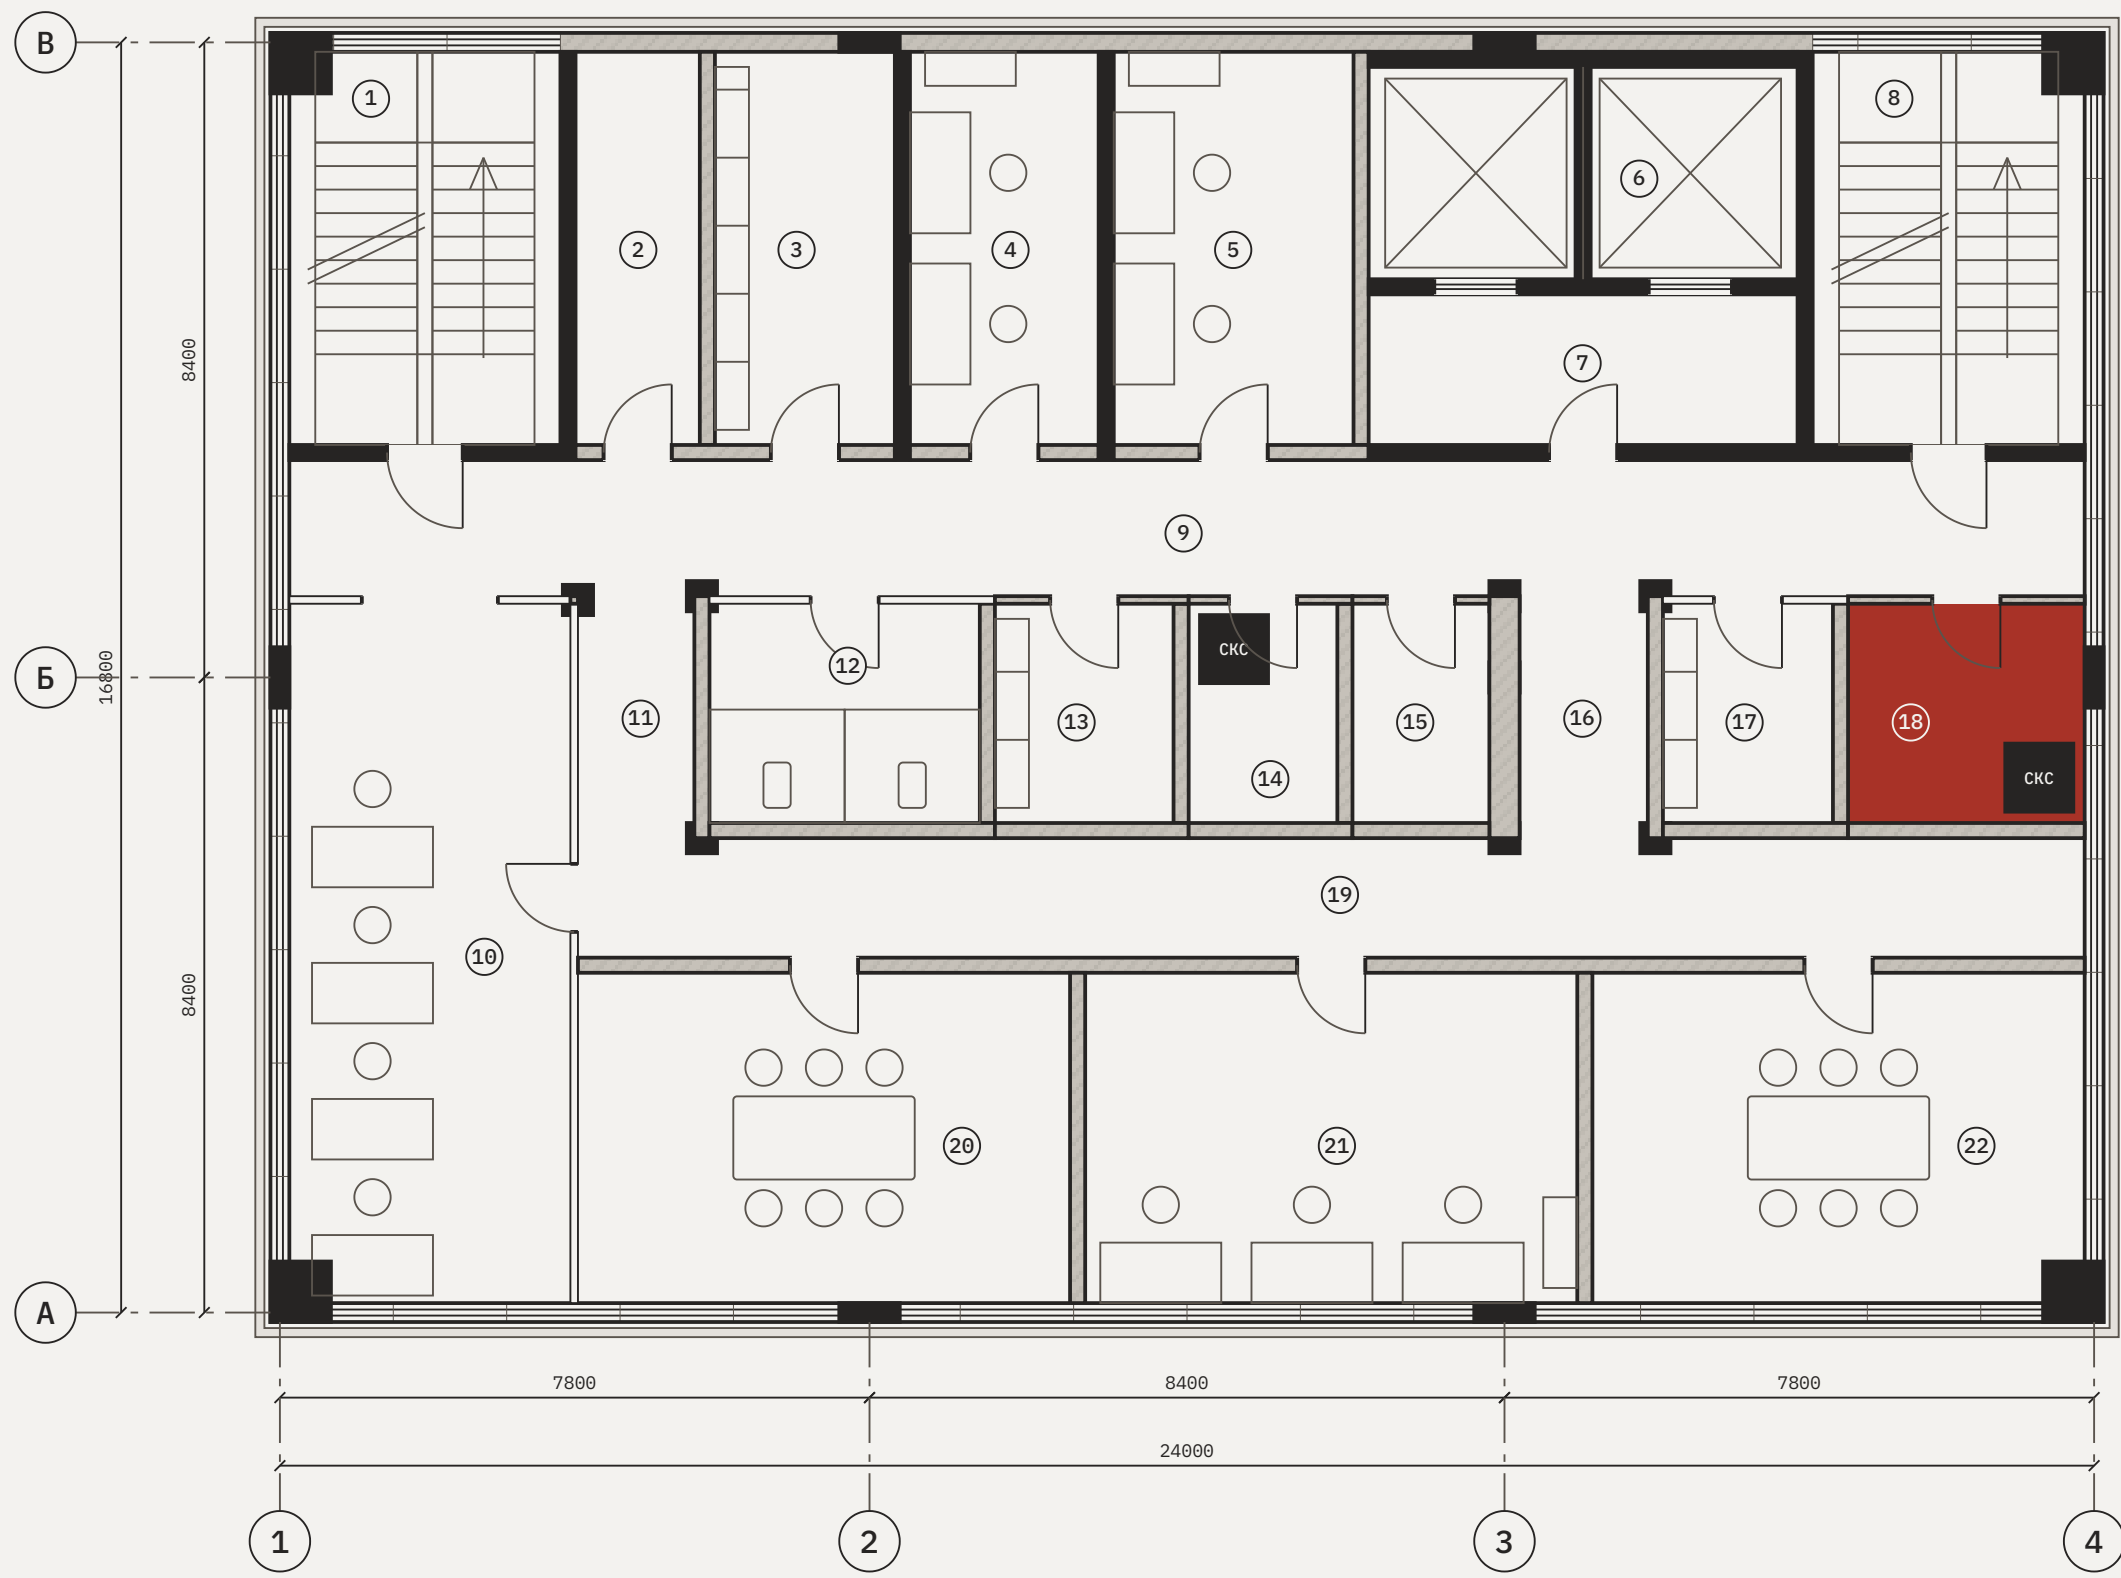

ПЛАН ЭТАЖА НА ОТМ. +0,000
М 1:100

ЭКСПЛИКАЦИЯ ПОМЕЩЕНИЙ

№	НАИМЕНОВАНИЕ	РМ	ПЛОЩАДЬ, М²
1	Лестничная клетка ЛК-1	—	18,65
2	Кладовая	—	8,55
3	Архив	—	12,38
4	Кабинет 2	2	12,98
5	Кабинет 1	2	16,49
6	Шахта на 2 лифта	—	15,93
7	Тамбур-шлюз лифтового холла	—	11,30
8	Лестничная клетка ЛК-2	—	18,71
9	Коридор главный	—	42,75
10	Опенспейс	5	34,39
11	Коридор-связь КЗ	—	4,93
12	Санузел	—	10,37
13	Подсобное помещение	—	6,85
14	Кроссовая СКС	—	4,89
15	Кухня-буфет	—	5,25
16	Коридор-связь К4	—	5,43
17	Электрощитовая	—	6,52
18	Серверная	—	8,27
19	Коридор продольный	—	31,51
20	Переговорная малая	—	28,44
21	Кабинет 3	3	28,44
22	Переговорная	—	28,45
ИТОГО ПОЛЕЗНАЯ		12	345,55
ПЛОЩАДЬ ЭТАЖА В ОСЯХ			403,20

УСЛОВНЫЕ ОБОЗНАЧЕНИЯ

- Пилоны, стены ядра, стояки – монолитный ж/б
- Заполнение и внутренние стены – блоки
- Перегородки светопрозрачные
- Ленточное остекление, навесной фасад
- Серверная – предмет решения листа

Красная заливка на листе несёт один смысл – серверная.
«СКС» – вертикальные стояки слаботочных сетей: связь этажа с основной и резервной серверными на других этажах.
Оборудование, шкафы и кабельные трассы не показаны – они являются предметом разработки.
«РМ» – число рабочих мест в помещении.
Шахта лифтов в полезную площадь не входит.
Размеры в миллиметрах. Лист бюро, режим Б.

V03
ВАРИАНТ
403 М²