


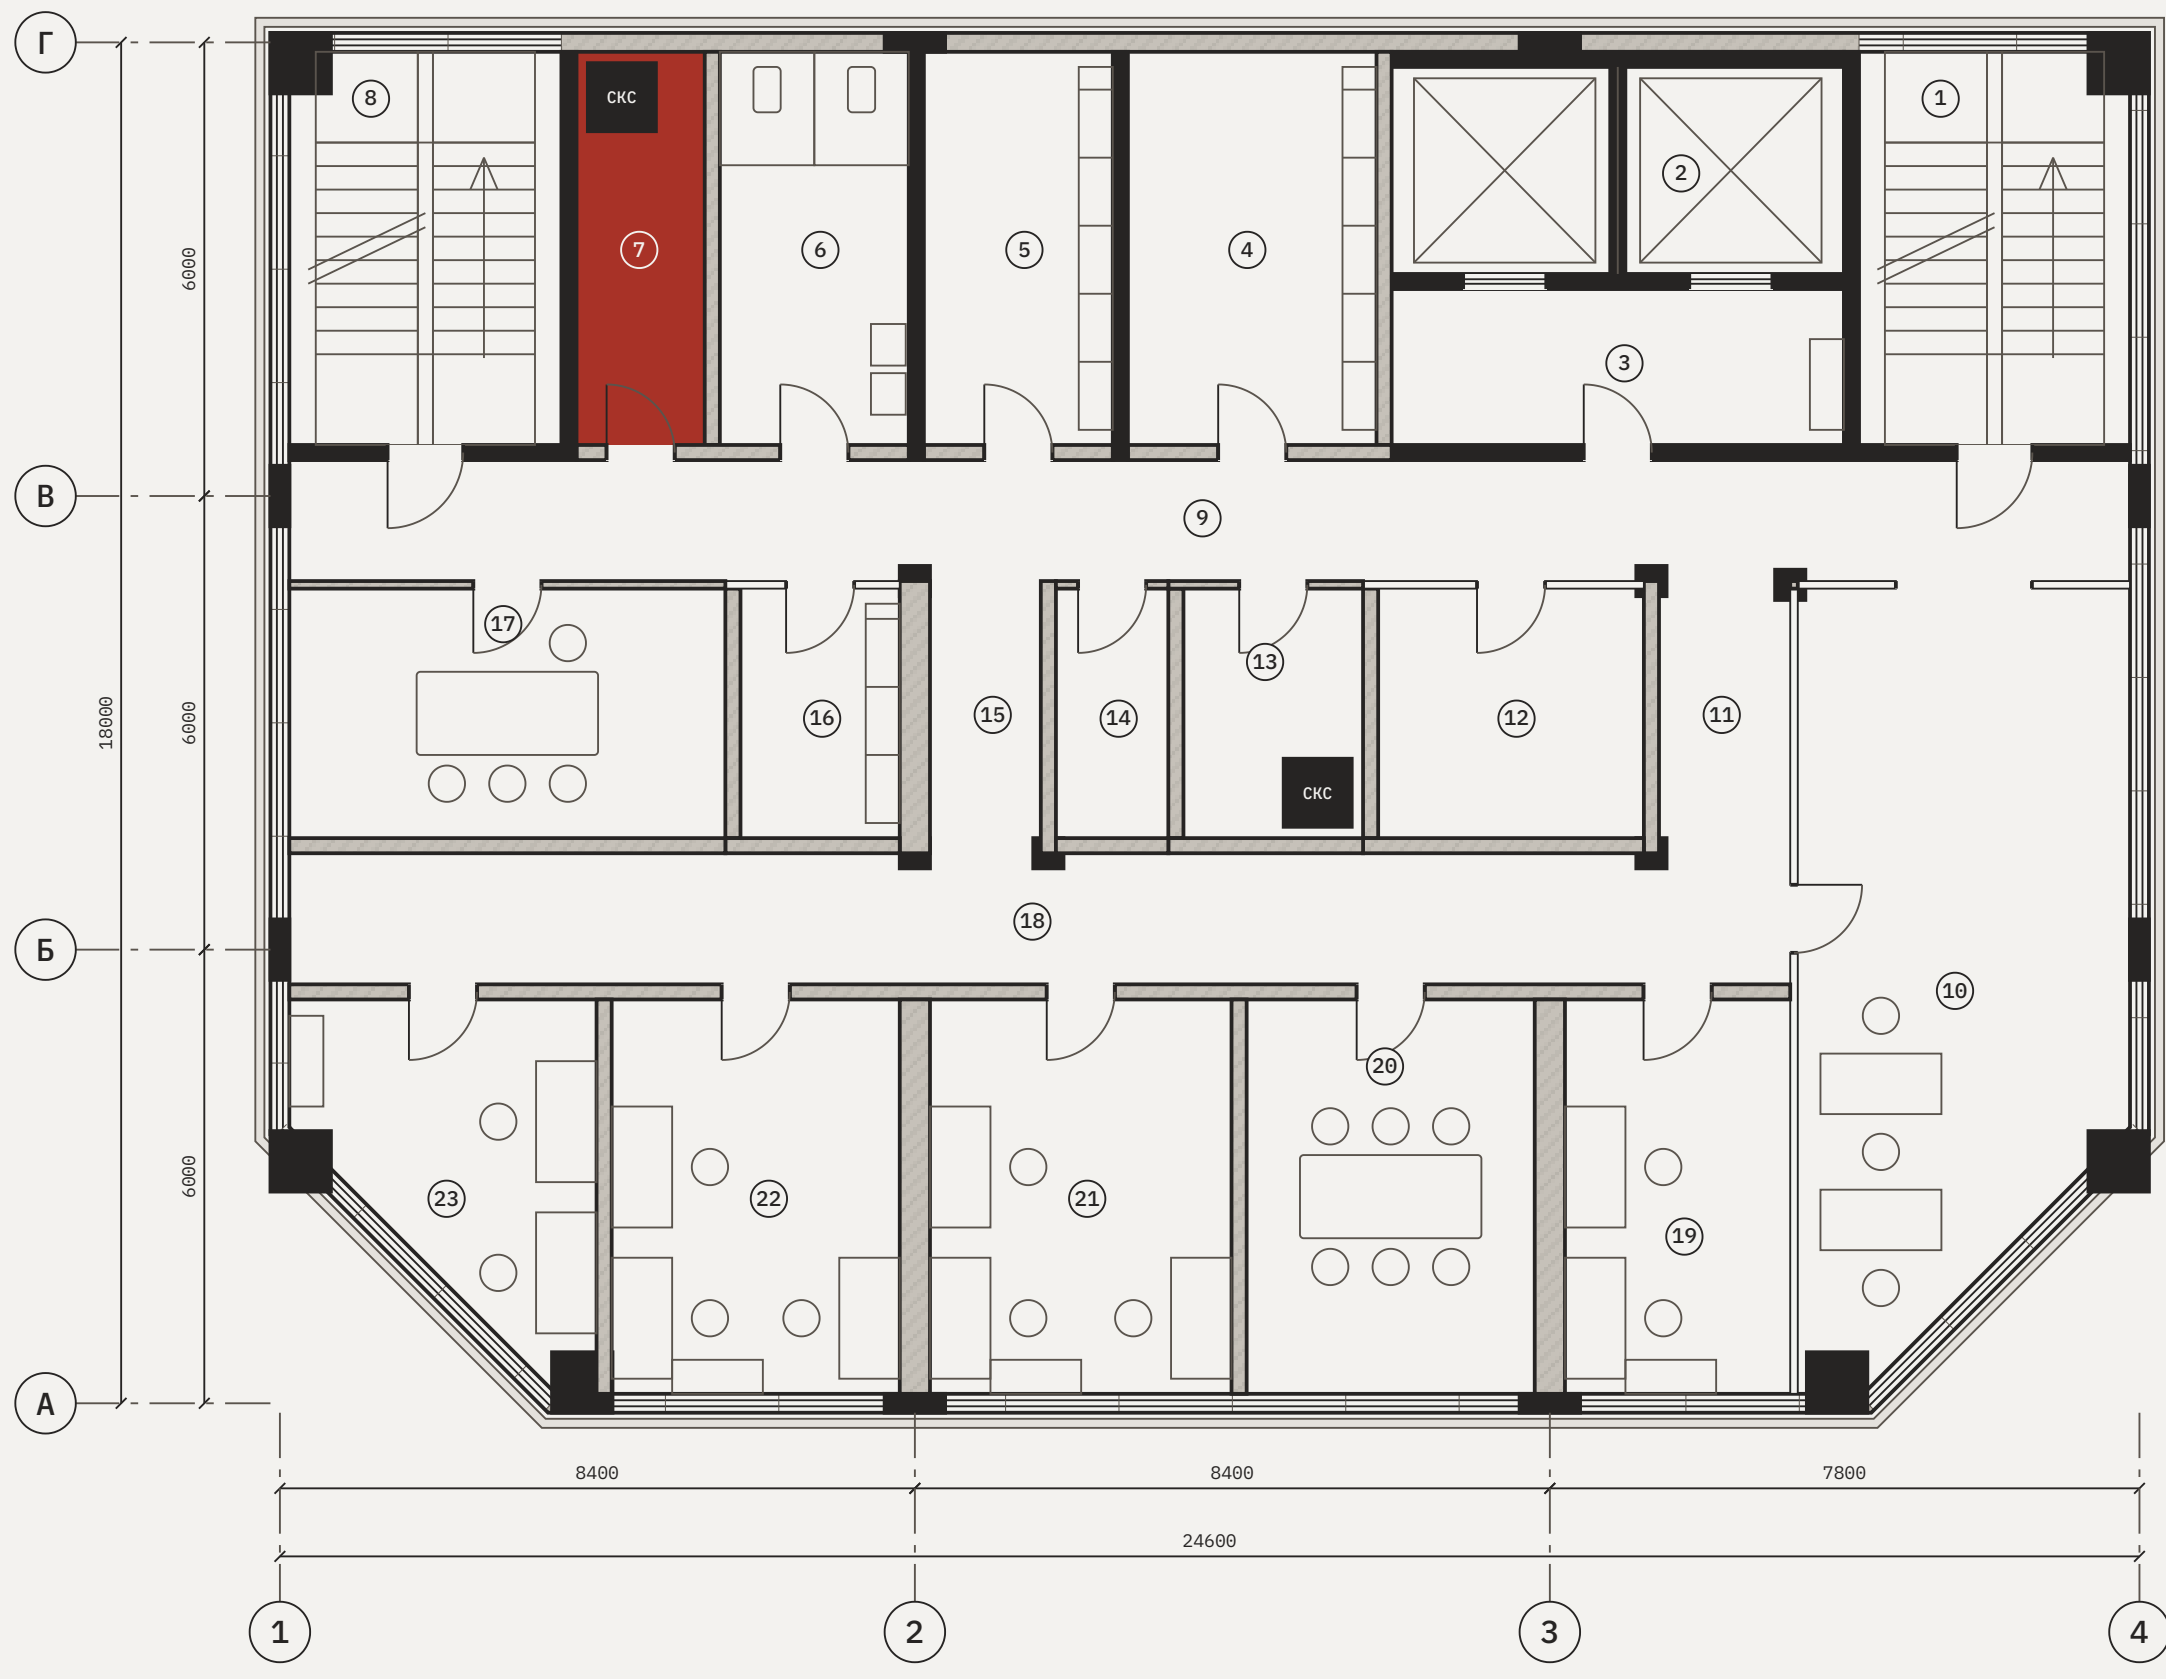

ПЛАН ЭТАЖА НА ОТМ. +0,000

М 1:100

ЭКСПЛИКАЦИЯ ПОМЕЩЕНИЙ

№	НАИМЕНОВАНИЕ	РМ	ПЛОЩАДЬ, М²
1	Лестничная клетка ЛК-1	—	18,64
2	Шахта на 2 лифта	—	16,38
3	Кабинет 5	1	12,34
4	Архив	—	17,10
5	Электрощитовая	—	12,99
6	Санузел	—	12,99
7	Серверная	—	8,01
8	Лестничная клетка ЛК-2	—	18,71
9	Коридор главный	—	38,96
10	Опенспейс	5	40,59
11	Коридор-связь КЗ	—	6,25
12	Тамбур-шлюз лифтового холла	—	11,60
13	Кроссовая СКС	—	7,03
14	Подсобное помещение	—	4,91
15	Коридор-связь К4	—	5,28
16	Кухня-буфет	—	6,95
17	Переговорная малая	—	19,03
18	Коридор продольный	—	34,43
19	Кабинет 4	2	15,54
20	Переговорная	—	19,88
21	Кабинет 2	3	20,81
22	Кабинет 1	3	19,88
23	Кабинет 3	2	14,98
ИТОГО ПОЛЕЗНАЯ		16	366,90
ПЛОЩАДЬ ЭТАЖА В ОСЯХ			429,84

УСЛОВНЫЕ ОБОЗНАЧЕНИЯ

- Пилоны, стены ядра, стояки – монолитный ж/б
- Заполнение и внутренние стены – блоки
- Пперегородки светопрозрачные
- Ленточное остекление, навесной фасад
- Серверная – предмет решения листа

Красная заливка на листе несёт один смысл – серверная.
«СКС» – вертикальные стояки слаботочных сетей: связь этажа с основной и резервной серверными на других этажах.
Оборудование, шкафы и кабельные трассы не показаны – они являются предметом разработки.
«РМ» – число рабочих мест в помещении.
Шахта лифтов в полезную площадь не входит.
Размеры в миллиметрах. Лист бюро, режим Б.

V21
ВАРИАНТ
430 М²