


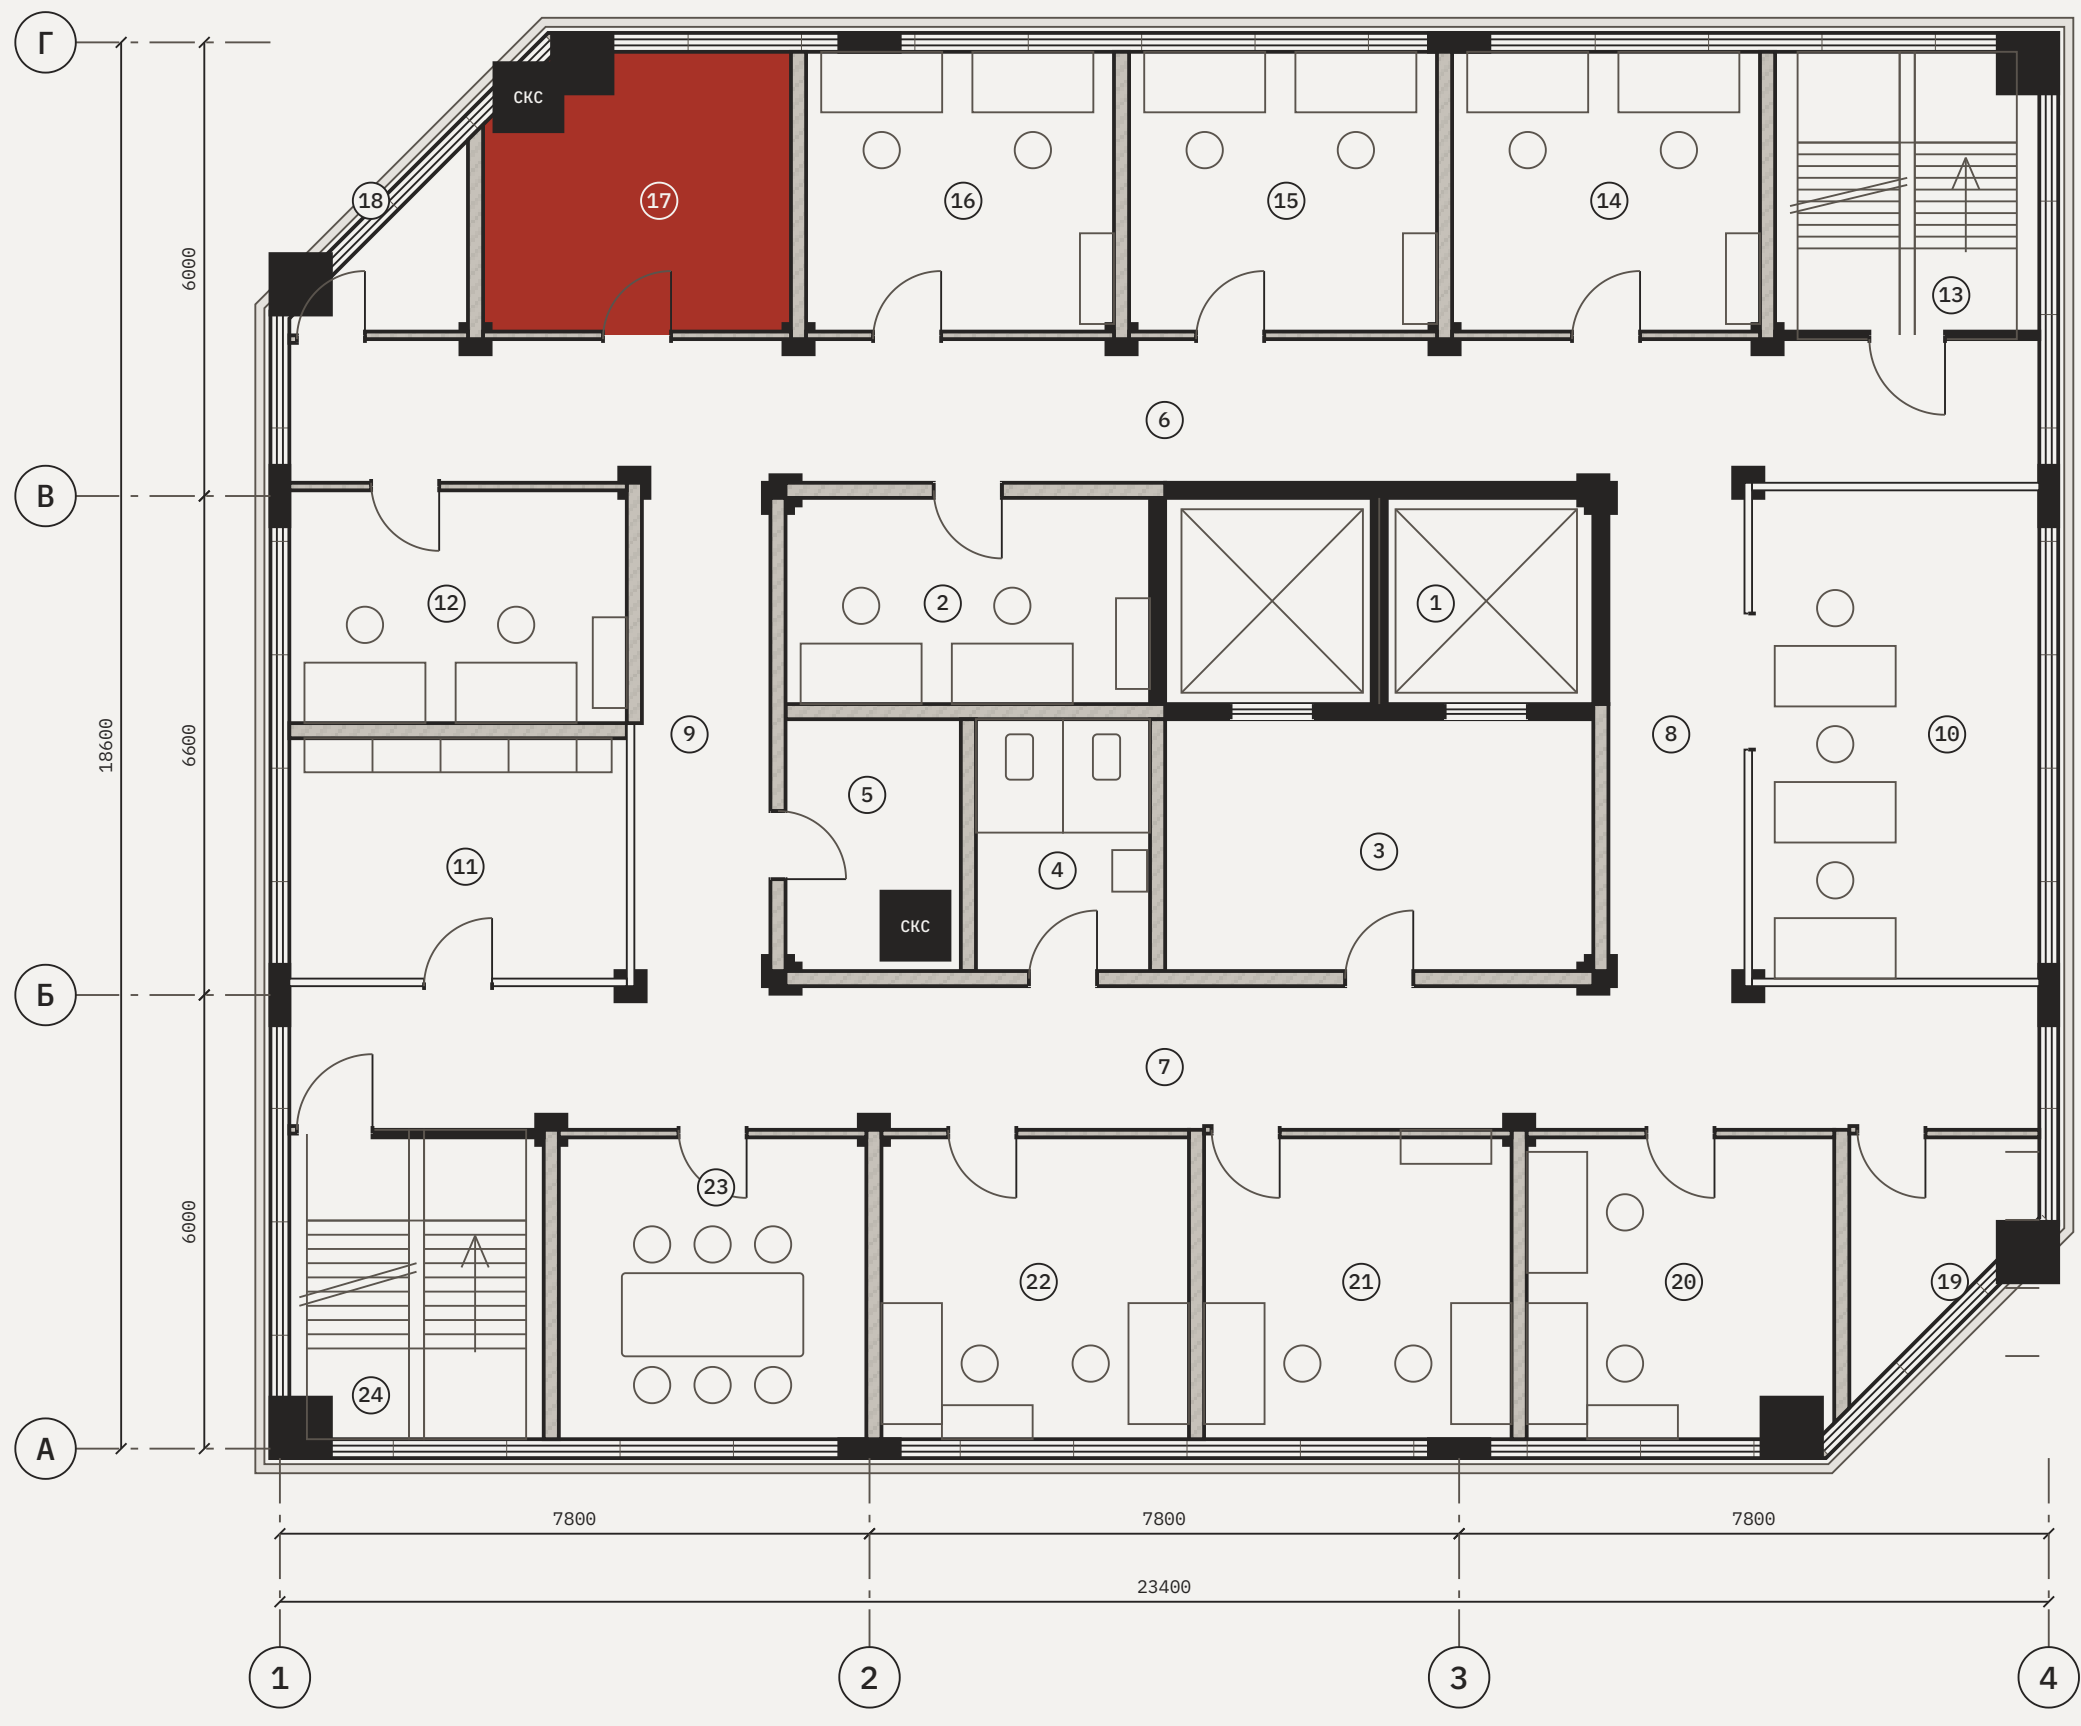

ПЛАН ЭТАЖА НА ОТМ. +0,000

М 1:100

ЭКСПЛИКАЦИЯ ПОМЕЩЕНИЙ

№	НАИМЕНОВАНИЕ	РМ	ПЛОЩАДЬ, М²
1	Шахта на 2 лифта	—	15,45
2	Кабинет 8	2	13,15
3	Тамбур-шлюз лифтового холла	—	18,87
4	Санузел	—	7,67
5	Кроссовая СКС	—	6,91
6	Коридор северный	—	43,98
7	Коридор южный	—	43,98
8	Коридор западный	—	12,65
9	Коридор восточный	—	12,65
10	Опенспейс	4	25,30
11	Подсобное помещение	—	14,64
12	Кабинет 7	2	14,19
13	Лестничная клетка	—	13,28
14	Кабинет 3	2	15,48
15	Кабинет 5	2	15,48
16	Кабинет 4	2	15,48
17	Серверная	—	14,20
18	Копировальная	—	3,44
19	Кухня-буфет	—	6,09
20	Кабинет 1	2	16,62
21	Кабинет 2	2	16,65
22	Кабинет 6	2	16,65
23	Переговорная	—	16,65
24	Лестничная клетка	—	13,77
ИТОГО ПОЛЕЗНАЯ		20	377,78
ПЛОЩАДЬ ЭТАЖА В ОСЯХ			424,26

УСЛОВНЫЕ ОБОЗНАЧЕНИЯ

- Пилоны, стены ядра, стояки — монолитный ж/б
- Заполнение и внутренние стены — блоки
- Перегородки светопрозрачные
- Ленточное остекление, навесной фасад
- Серверная — предмет решения листа

Красная заливка на листе несёт один смысл — серверная.
«СКС» — вертикальные стояки слаботочных сетей: связь этажа с основной и резервной серверными на других этажах.
Оборудование, шкафы и кабельные трассы не показаны — они являются предметом разработки.
«РМ» — число рабочих мест в помещении.
Шахта лифтов в полезную площадь не входит.
Размеры в миллиметрах. Лист бюро, режим Б.

V53
ВАРИАНТ
424 М²