


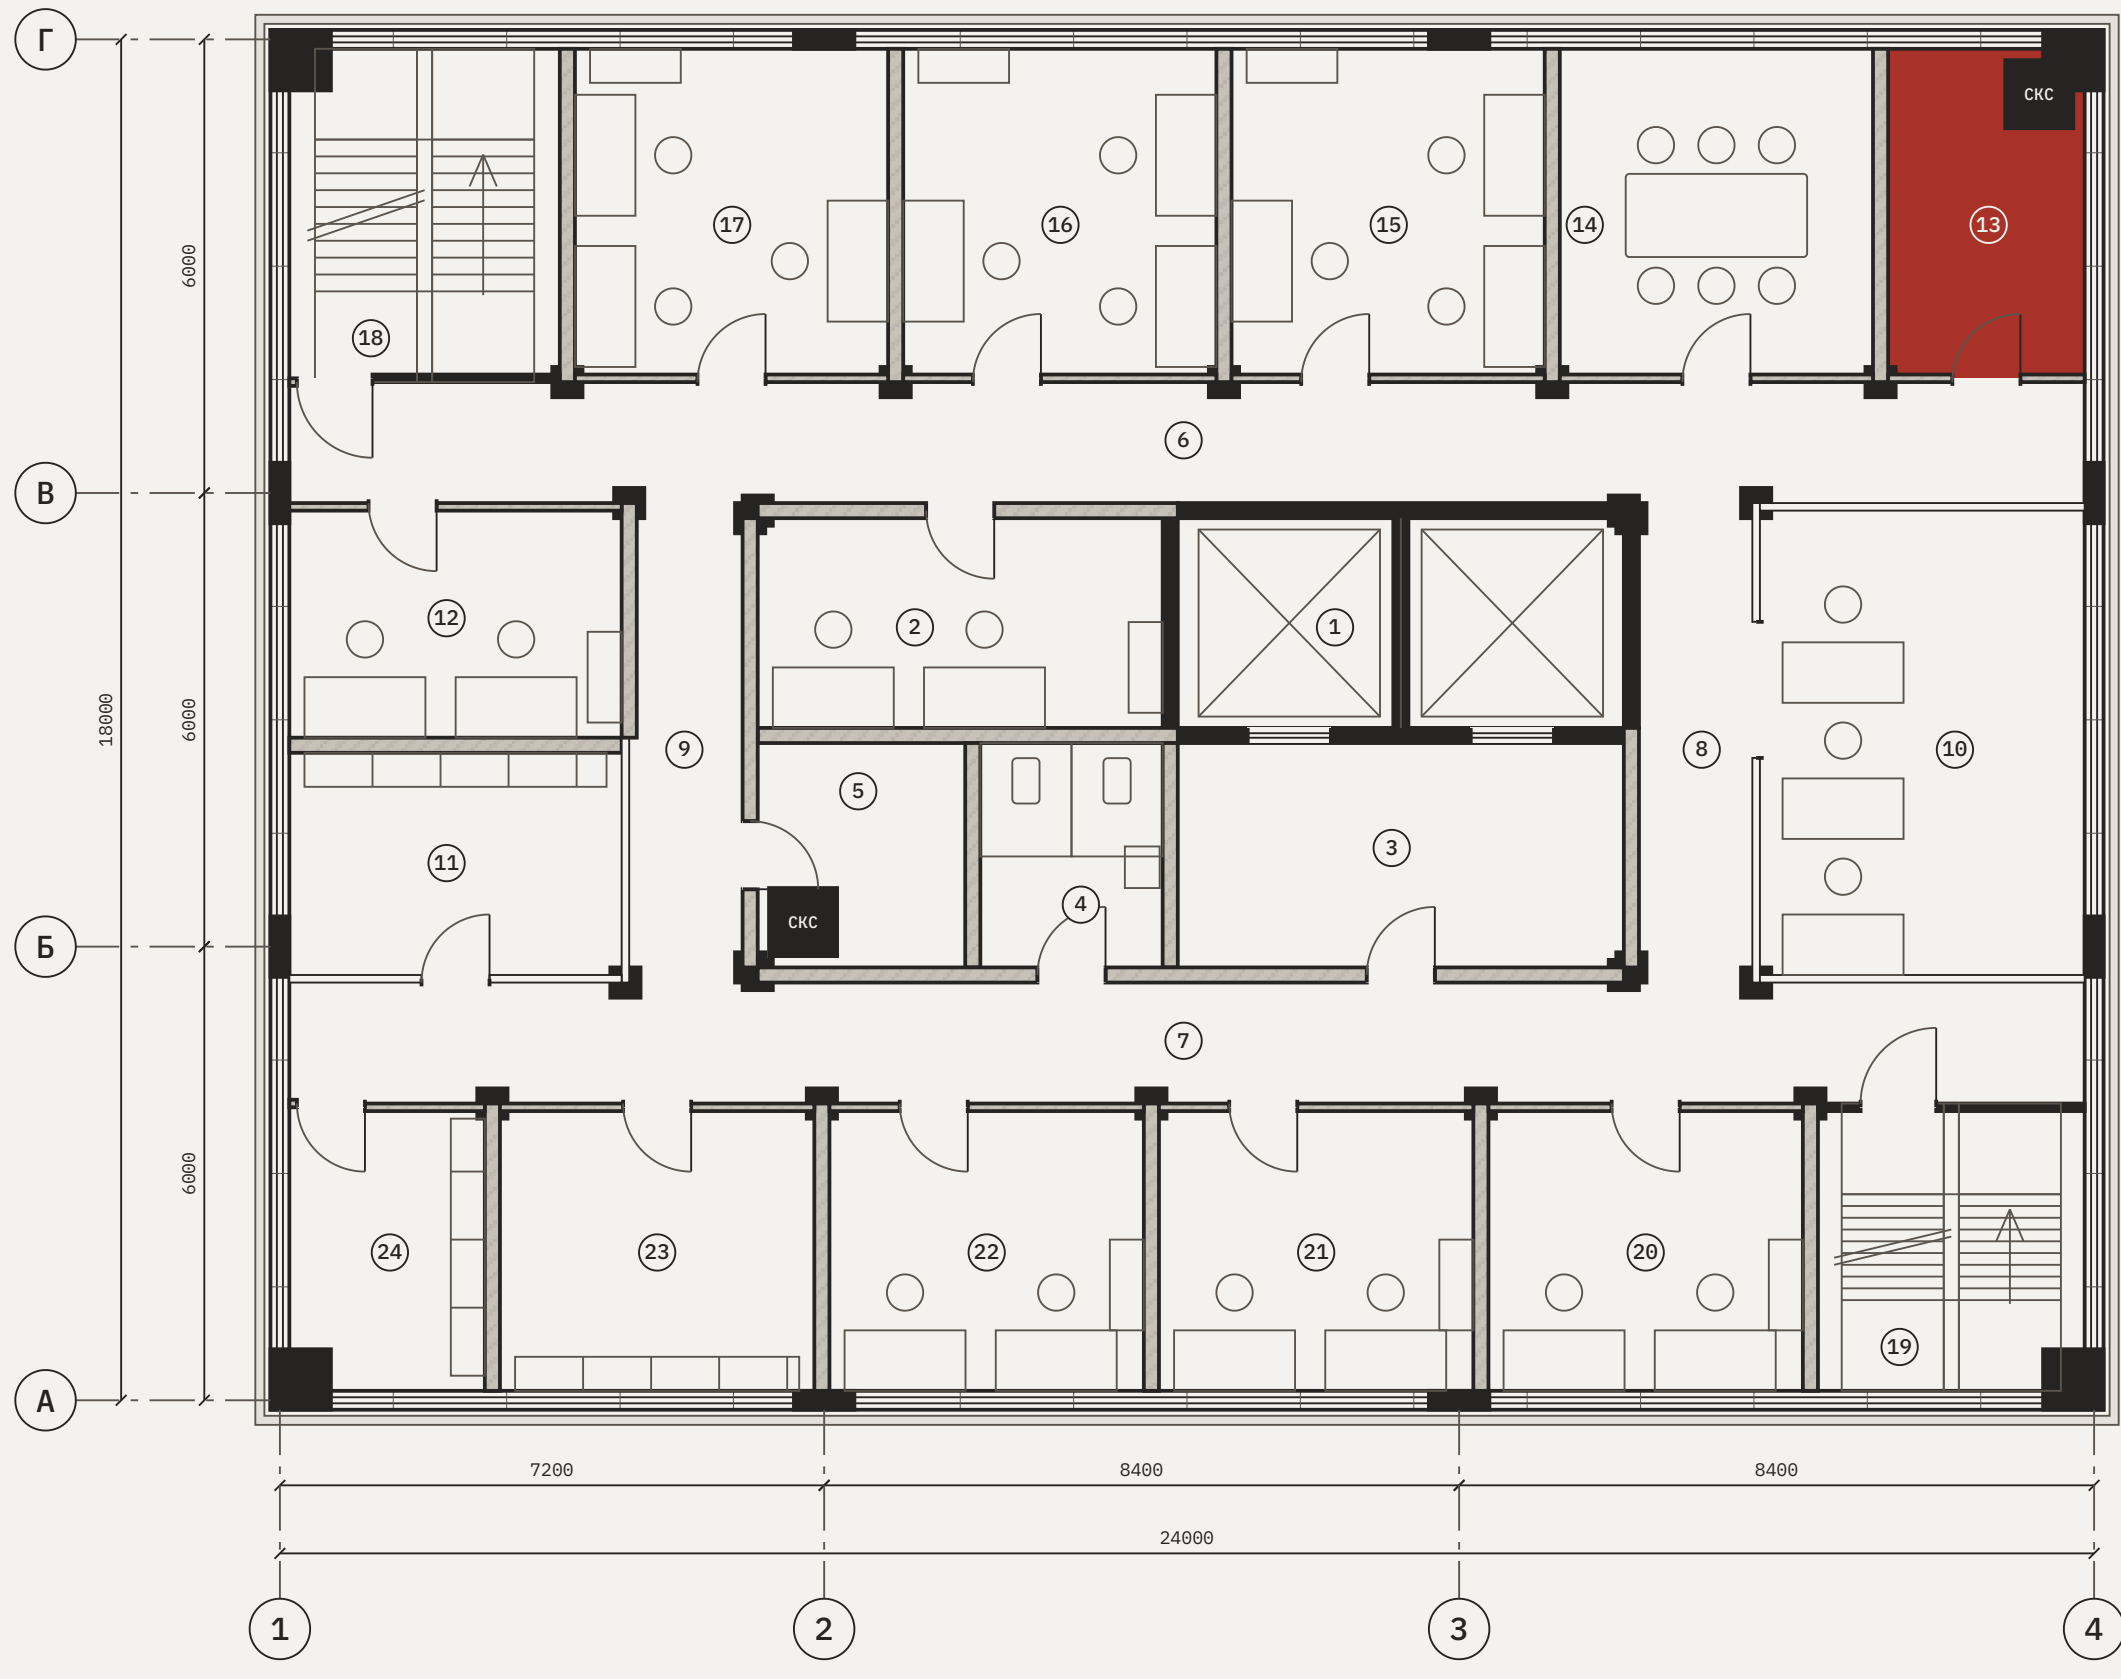

ПЛАН ЭТАЖА НА ОТМ. +0,000
М 1:100

ЭКСПЛИКАЦИЯ ПОМЕЩЕНИЙ

№	НАИМЕНОВАНИЕ	РМ	ПЛОЩАДЬ, М²
1	Шахта на 2 лифта	—	16,37
2	Кабинет 7	2	14,86
3	Тамбур-шлюз лифтового холла	—	17,51
4	Санузел	—	7,16
5	Кроссовая СКС	—	7,34
6	Коридор северный	—	38,00
7	Коридор южный	—	38,00
8	Коридор западный	—	10,15
9	Коридор восточный	—	10,15
10	Опенспейс	5	27,25
11	Кладовая	—	13,36
12	Кабинет 8	2	13,64
13	Серверная	—	10,65
14	Переговорная	—	18,26
15	Кабинет 1	3	18,26
16	Кабинет 3	3	18,26
17	Кабинет 6	3	18,26
18	Лестничная клетка	—	15,77
19	Лестничная клетка	—	13,41
20	Кабинет 5	2	15,80
21	Кабинет 2	2	15,80
22	Кабинет 4	2	15,80
23	Кладовая уборочного инвентаря	—	15,80
24	Кухня-буфет	—	9,83
ИТОГО ПОЛЕЗНАЯ		24	383,32
ПЛОЩАДЬ ЭТАЖА В ОСЯХ			432,00

УСЛОВНЫЕ ОБОЗНАЧЕНИЯ

- Пилоны, стены ядра, стояки — монолитный ж/б
- Заполнение и внутренние стены — блоки
- Перегородки светопрозрачные
- Ленточное остекление, навесной фасад
- Серверная — предмет решения листа

Красная заливка на листе несёт один смысл — серверная.
«СКС» — вертикальные стояки слаботочных сетей: связь этажа с основной и резервной серверными на других этажах.
Оборудование, шкафы и кабельные трассы не показаны — они являются предметом разработки.
«РМ» — число рабочих мест в помещении.
Шахта лифтов в полезную площадь не входит.
Размеры в миллиметрах. Лист бюро, режим Б.

V57
ВАРИАНТ
432 М²