


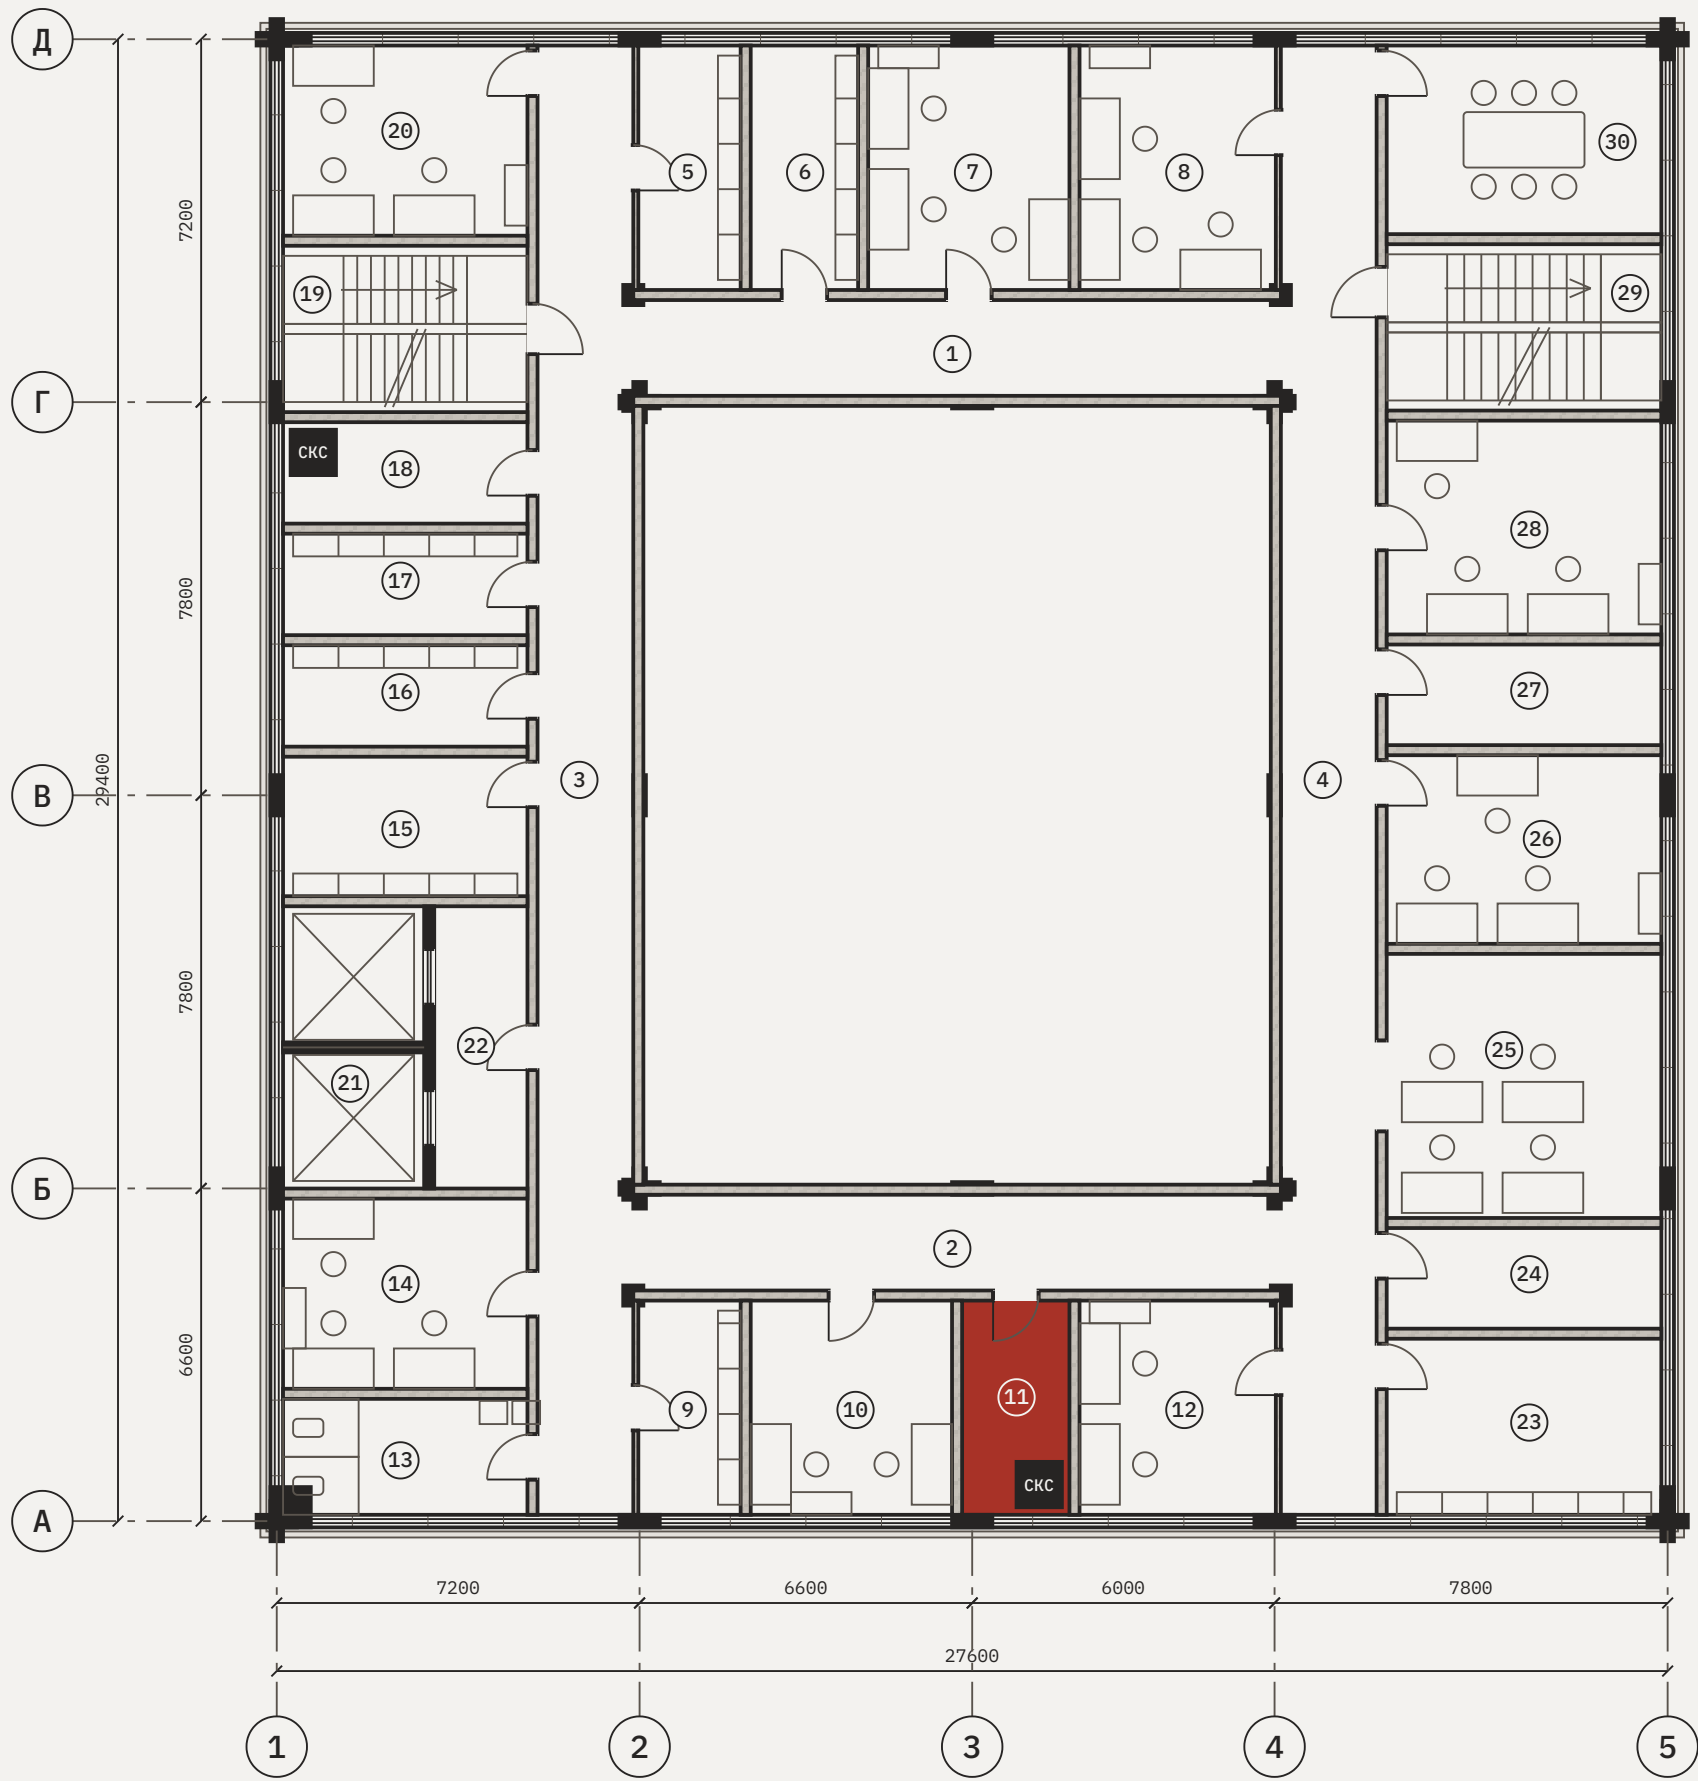

ПЛАН ЭТАЖА НА ОТМ. +0,000
М 1:150

ЭКСПЛИКАЦИЯ ПОМЕЩЕНИЙ

№	НАИМЕНОВАНИЕ	РМ	ПЛОЩАДЬ, М²
1	Коридор северный	—	24,41
2	Коридор южный	—	24,41
3	Коридор западный	—	55,38
4	Коридор восточный	—	55,38
5	Кладовая	—	10,33
6	Подсобное помещение 6	—	10,34
7	Кабинет 4	3	19,37
8	Кабинет 5	3	19,38
9	Подсобное помещение 1	—	9,05
10	Кабинет 1	2	16,98
11	Серверная	—	8,24
12	Кабинет 7	2	16,98
13	Санузел	—	11,15
14	Кабинет 8	3	18,30
15	Кухня-буфет	—	13,42
16	Подсобное помещение 4	—	9,76
17	Подсобное помещение 5	—	9,76
18	Кроссовая СКС	—	8,95
19	Лестничная клетка ЛК-1	—	16,00
20	Кабинет 6	3	18,30
21	Шахта на 2 лифта	—	15,68
22	Тамбур-шлюз лифтового холла	—	10,36
23	Копировальная	—	19,04
24	Подсобное помещение 2	—	10,88
25	Опенспейс	6	28,55
26	Кабинет 3	3	20,39
27	Подсобное помещение 3	—	10,88
28	Кабинет 2	3	23,12
29	Лестничная клетка ЛК-2	—	17,98
30	Переговорная	—	20,39
ИТОГО ПОЛЕЗНАЯ		28	537,48
ПЛОЩАДЬ ЭТАЖА В ОСЯХ			614,88

УСЛОВНЫЕ ОБОЗНАЧЕНИЯ

- Пилоны, стены ядра, стояки — монолитный ж/б
- Заполнение и внутренние стены — блоки
- Перегородки светопрозрачные
- Ленточное остекление, навесной фасад
- Серверная — предмет решения листа

Красная заливка на листе несёт один смысл — серверная.
«СКС» — вертикальные стояки слаботочных сетей: связь этажа с основной и резервной серверными на других этажах.
Оборудование, шкафы и кабельные трассы не показаны — они являются предметом разработки.
«РМ» — число рабочих мест в помещении.
Шахта лифтов в полезную площадь не входит.
Размеры в миллиметрах. Лист бюро, режим Б.

V58
ВАРИАНТ
615 М²