


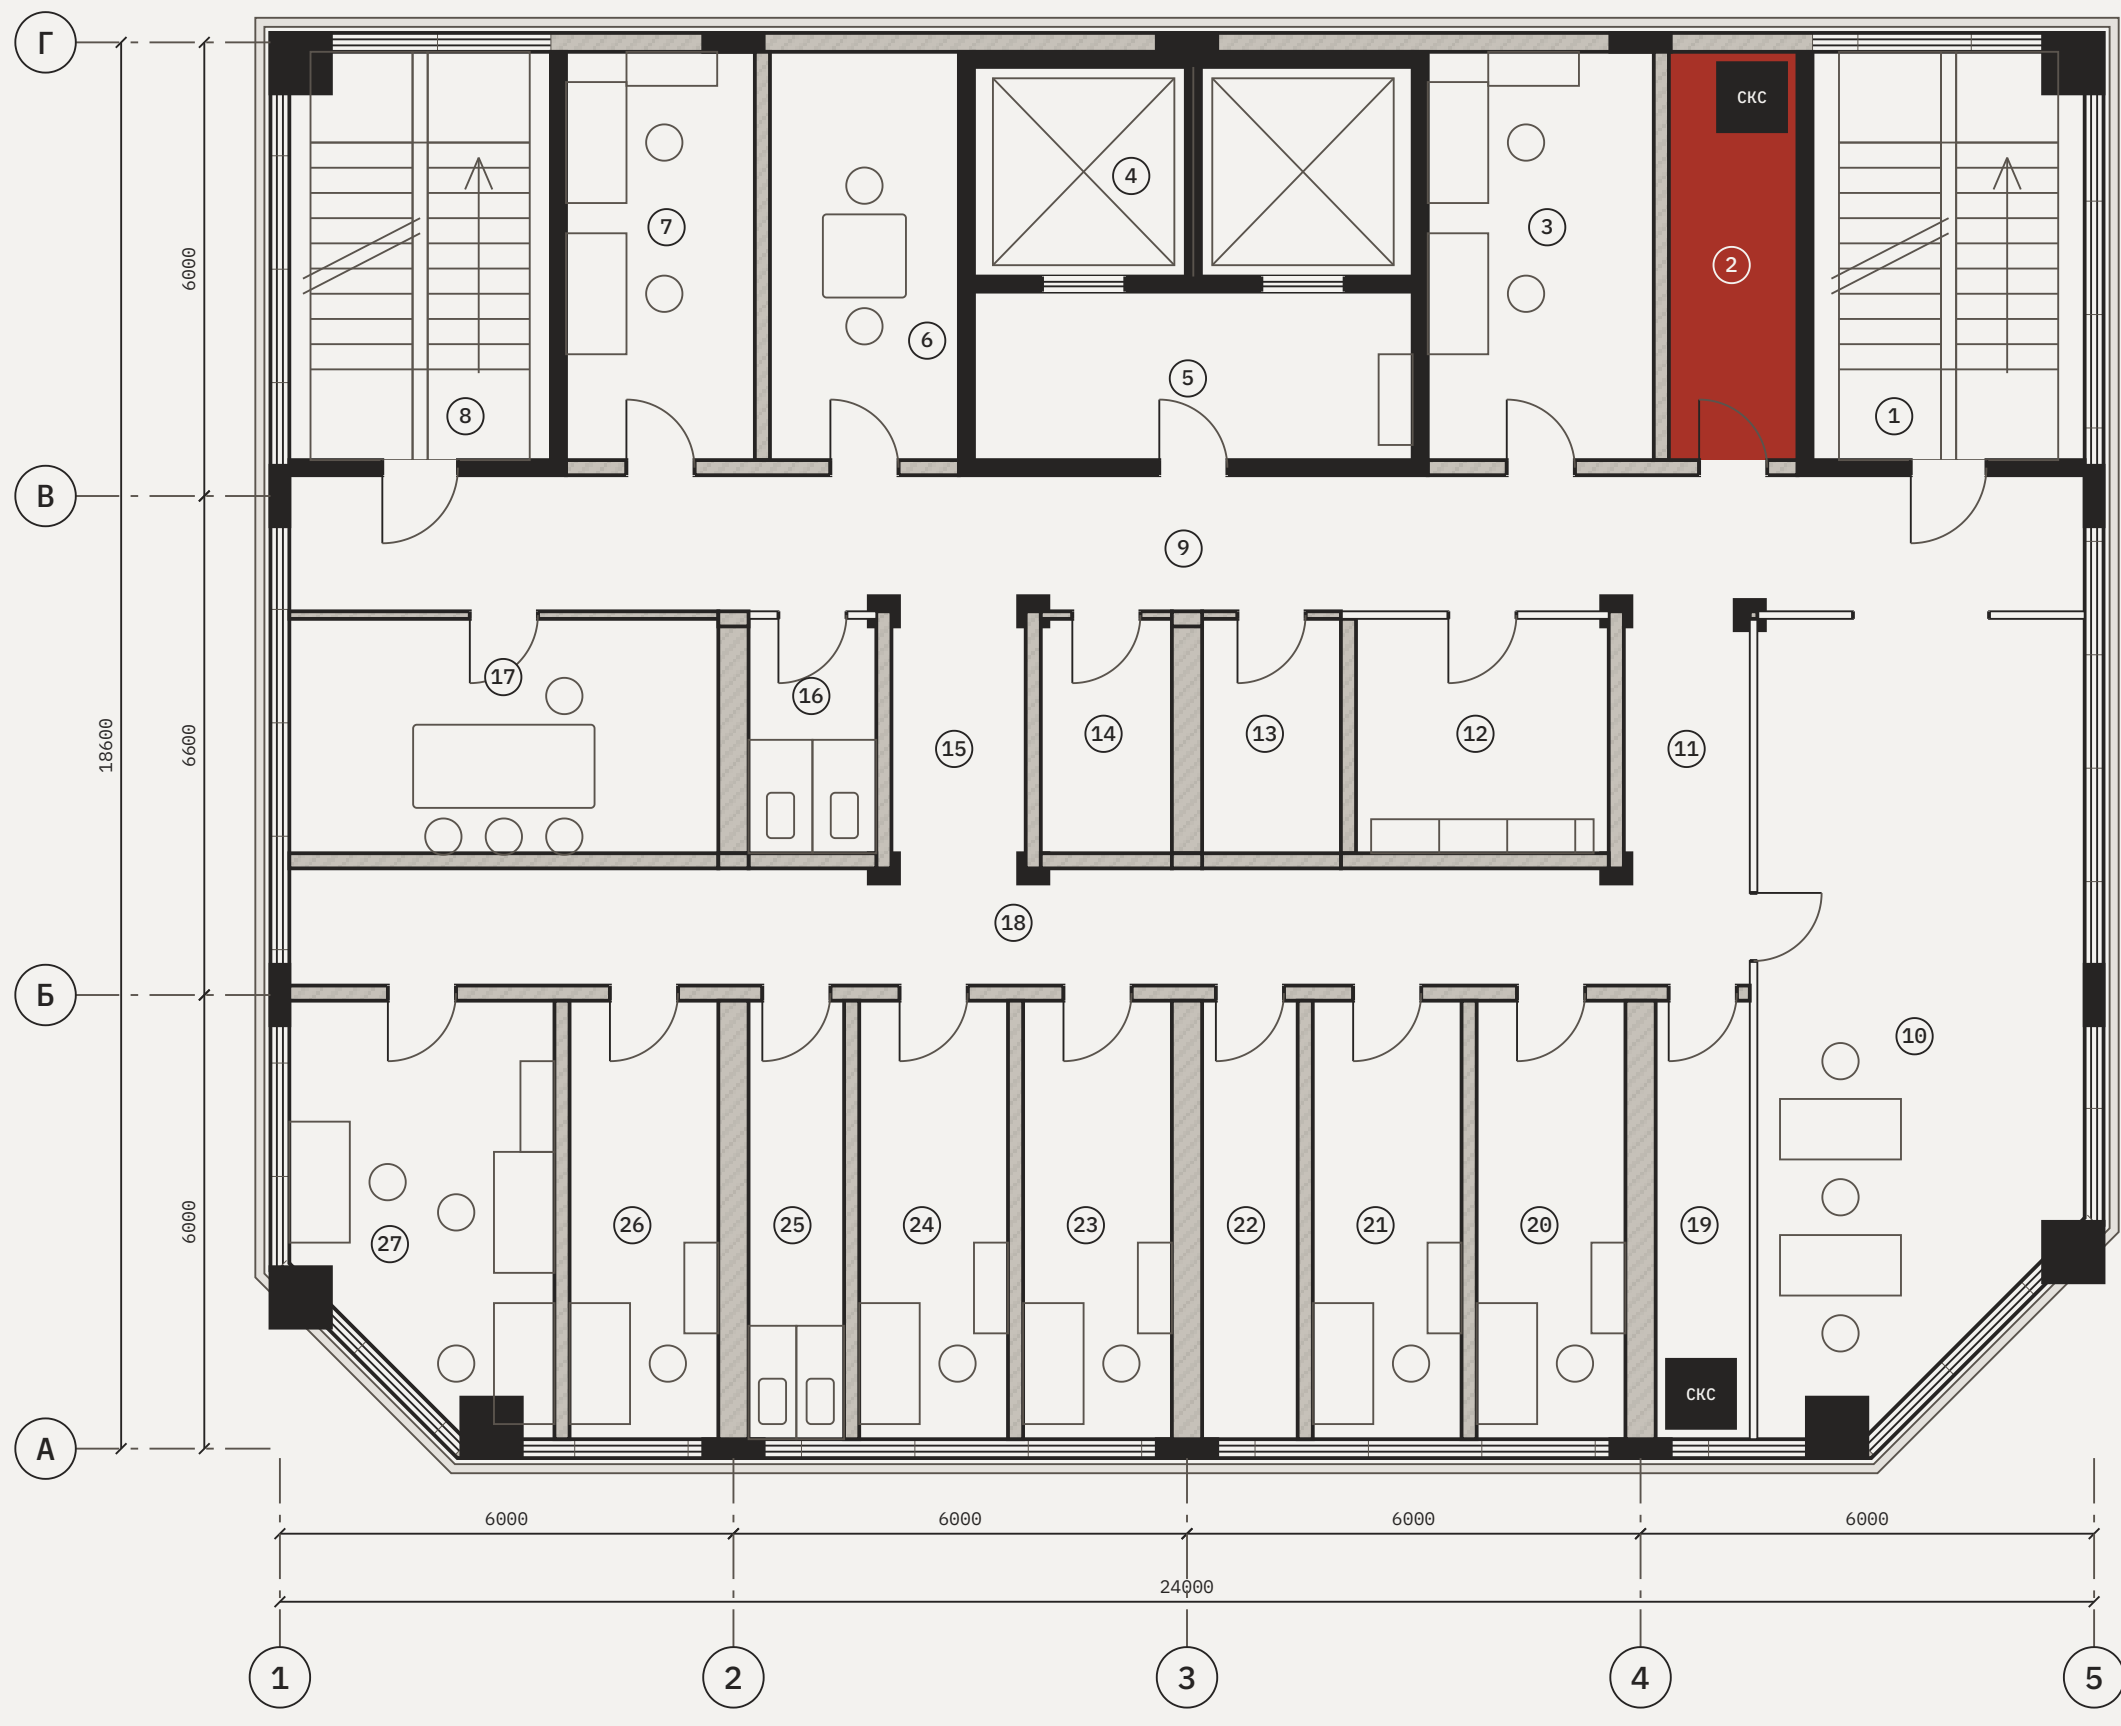

ПЛАН ЭТАЖА НА ОТМ. +0,000

М 1:100

ЭКСПЛИКАЦИЯ ПОМЕЩЕНИЙ

№	НАИМЕНОВАНИЕ	РМ	ПЛОЩАДЬ, М²
1	Лестничная клетка ЛК-1	—	19,44
2	Серверная	—	8,37
3	Кабинет 1	2	16,15
4	Шахта на 2 лифта	—	16,09
5	Кабинет 5	1	12,93
6	Переговорная малая	—	13,49
7	Кабинет 2	2	13,49
8	Лестничная клетка ЛК-2	—	18,68
9	Коридор главный	—	42,75
10	Опенспейс	7	42,70
11	Коридор-связь К3	—	5,66
12	Кладовая	—	10,36
13	Электрощитовая	—	5,69
14	Кухня-буфет	—	5,38
15	Коридор-связь К4	—	6,04
16	Санузел женский	—	5,24
17	Переговорная	—	17,59
18	Коридор продольный	—	29,95
19	Кроссовая СКС	—	6,41
20	Кабинет 3	1	11,41
21	Кабинет 6	1	11,41
22	Тамбур-шлюз лифтового холла	—	7,33
23	Кабинет 9	1	11,41
24	Кабинет 8	1	11,41
25	Санузел мужской	—	7,33
26	Кабинет 7	1	11,41
27	Кабинет 4	3	17,63
ИТОГО ПОЛЕЗНАЯ		20	369,66
ПЛОЩАДЬ ЭТАЖА В ОСЯХ			439,02

УСЛОВНЫЕ ОБОЗНАЧЕНИЯ

- Пилоны, стены ядра, стояки — монолитный ж/б
- Заполнение и внутренние стены — блоки
- Перегородки светопрозрачные
- Ленточное остекление, навесной фасад
- Серверная — предмет решения листа

Красная заливка на листе несёт один смысл — серверная.
«СКС» — вертикальные стояки слаботочных сетей: связь этажа с основной и резервной серверными на других этажах.
Оборудование, шкафы и кабельные трассы не показаны — они являются предметом разработки.
«РМ» — число рабочих мест в помещении.
Шахта лифтов в полезную площадь не входит.
Размеры в миллиметрах. Лист бюро, режим Б.

V61
ВАРИАНТ
439 М²