


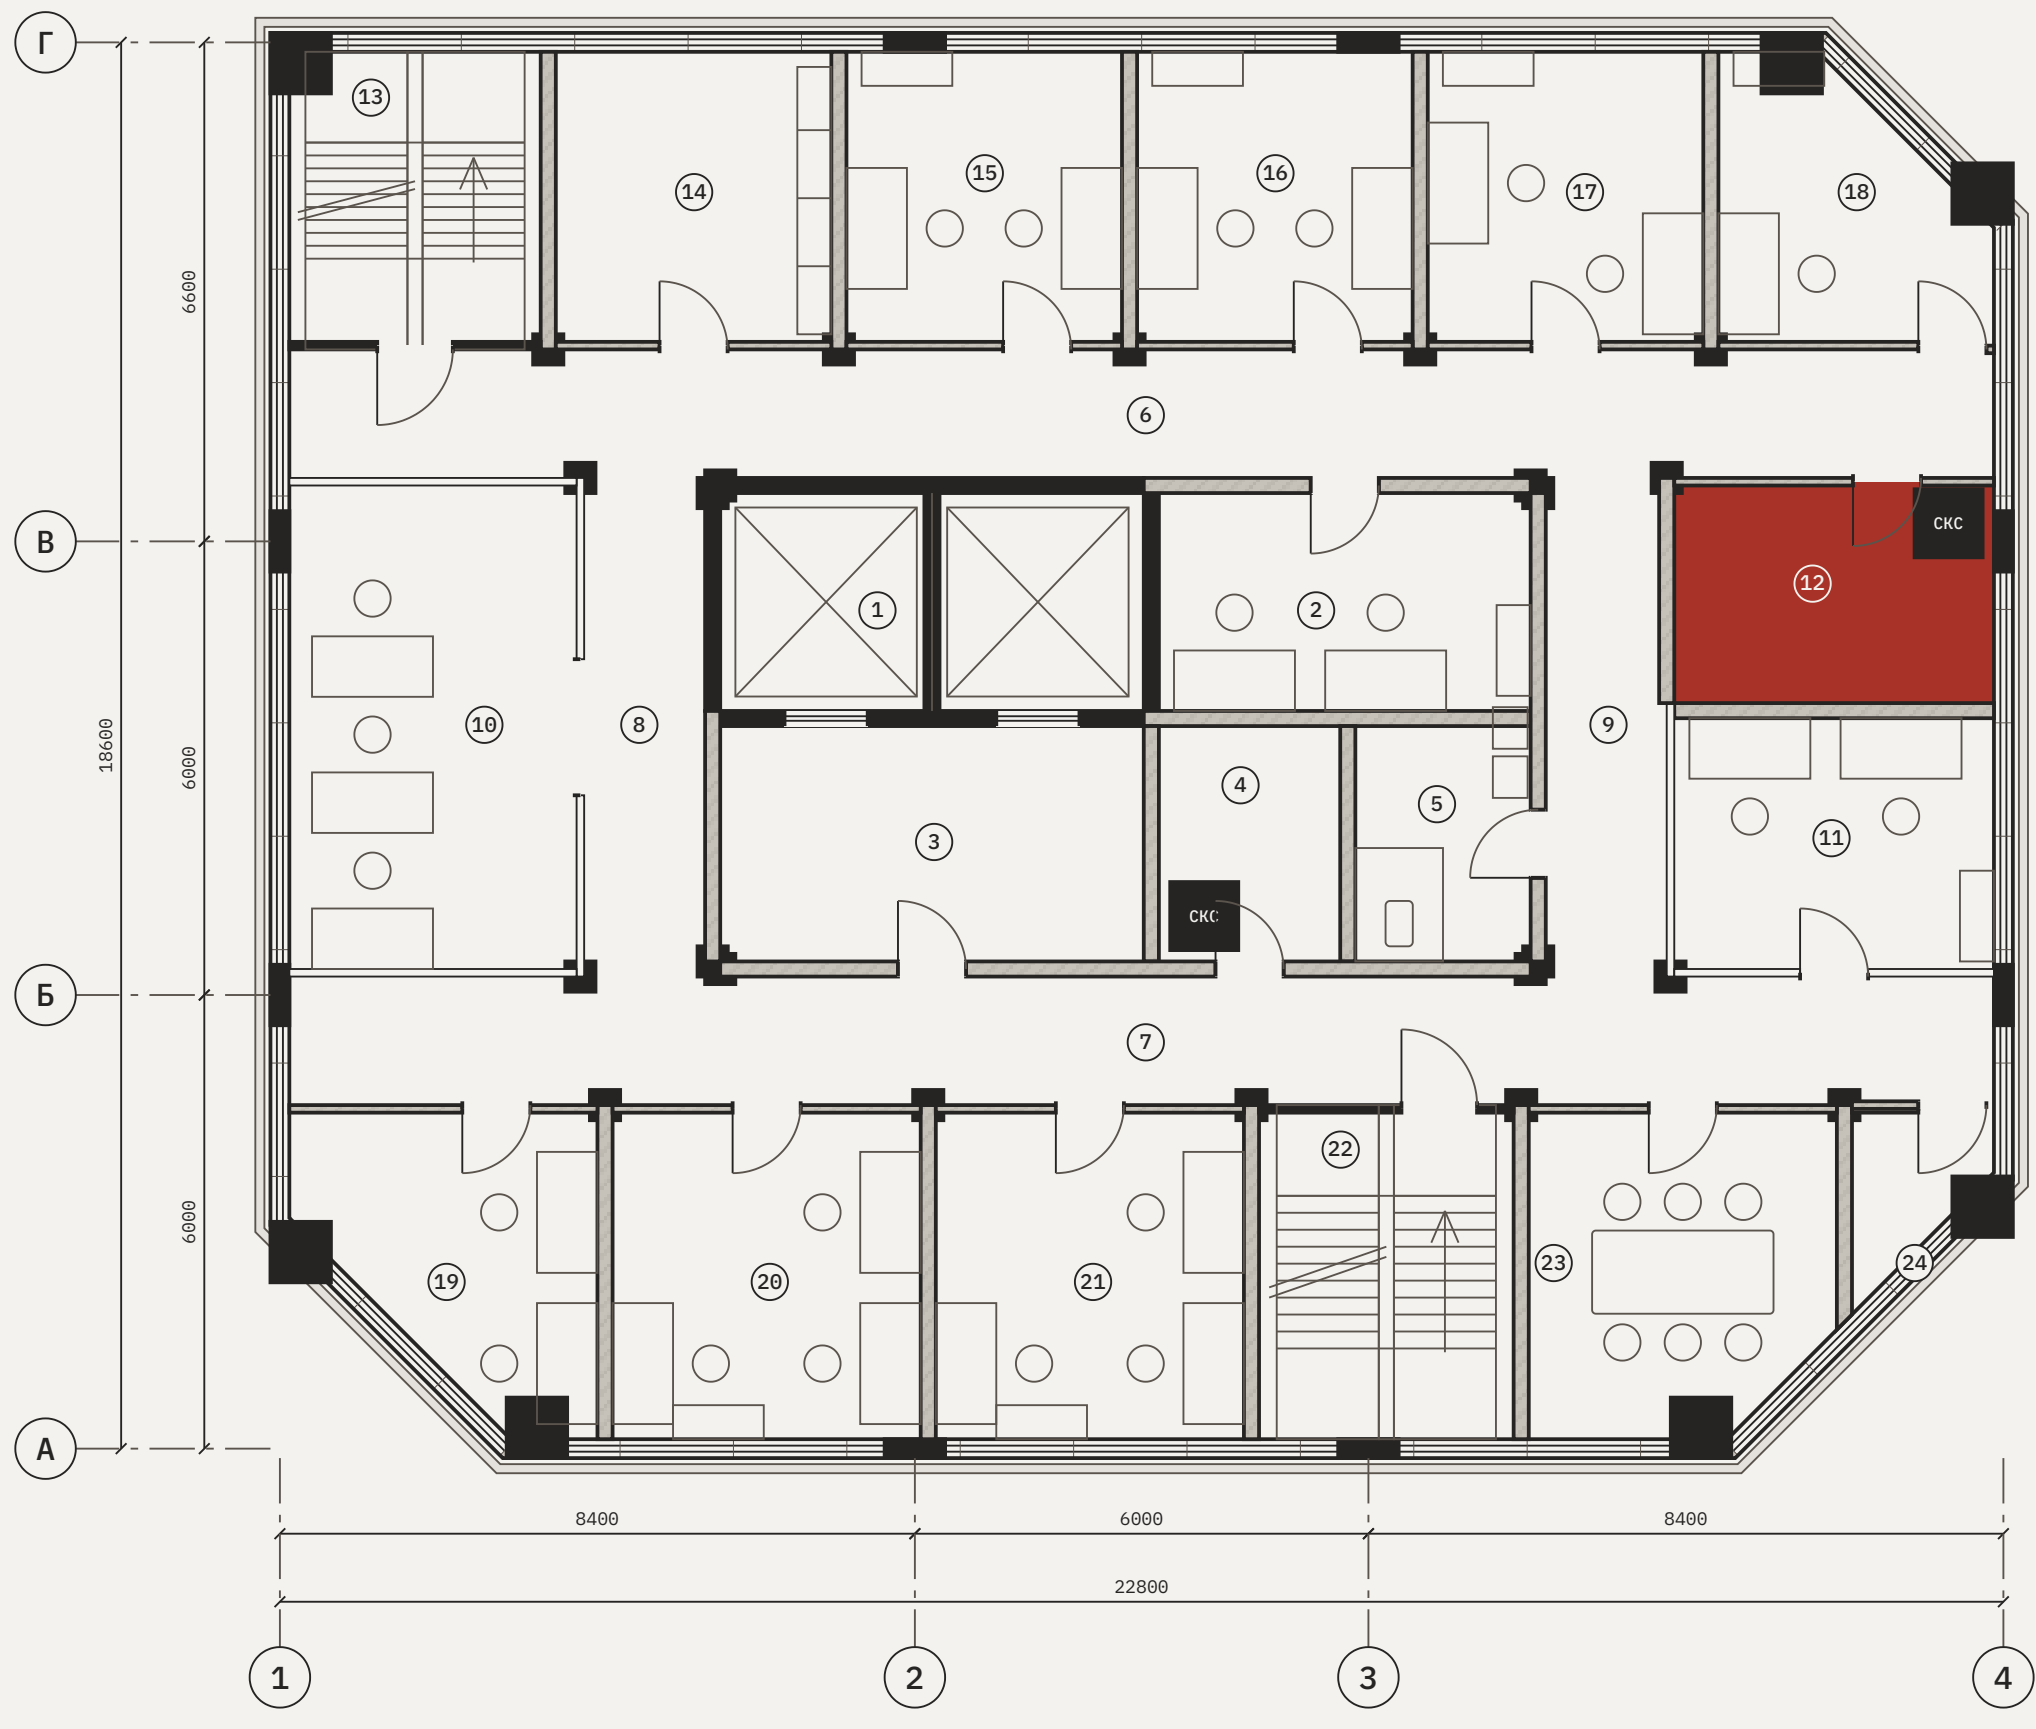

ПЛАН ЭТАЖА НА ОТМ. +0,000

М 1:100

ЭКСПЛИКАЦИЯ ПОМЕЩЕНИЙ

№	НАИМЕНОВАНИЕ	РМ	ПЛОЩАДЬ, М²
1	Шахта на 2 лифта	—	16,15
2	Кабинет 6	2	14,17
3	Тамбур-шлюз лифтового холла	—	17,44
4	Кроссовая СКС	—	6,66
5	Санузел	—	7,22
6	Коридор северный	—	38,34
7	Коридор южный	—	38,34
8	Коридор западный	—	11,21
9	Коридор восточный	—	11,21
10	Опенспейс	5	25,06
11	Кабинет 4	2	14,45
12	Серверная	—	11,78
13	Лестничная клетка	—	13,09
14	Кухня-буфет	—	14,35
15	Кабинет 8	2	14,35
16	Кабинет 5	2	14,35
17	Кабинет 2	2	14,35
18	Кабинет 9	1	11,64
19	Кабинет 7	2	13,73
20	Кабинет 1	3	18,01
21	Кабинет 3	3	18,01
22	Лестничная клетка	—	14,88
23	Переговорная	—	16,96
24	Кладовая уборочного инвентаря	—	3,44
ИТОГО ПОЛЕЗНАЯ		24	363,04
ПЛОЩАДЬ ЭТАЖА В ОСЯХ			410,22

УСЛОВНЫЕ ОБОЗНАЧЕНИЯ

- Пилоны, стены ядра, стояки — монолитный ж/б
- Заполнение и внутренние стены — блоки
- Перегородки светопрозрачные
- Ленточное остекление, навесной фасад
- Серверная — предмет решения листа

Красная заливка на листе несёт один смысл — серверная.
«СКС» — вертикальные стояки слаботочных сетей: связь этажа с основной и резервной серверными на других этажах.
Оборудование, шкафы и кабельные трассы не показаны — они являются предметом разработки.
«РМ» — число рабочих мест в помещении.
Шахта лифтов в полезную площадь не входит.
Размеры в миллиметрах. Лист бюро, режим Б.

V63
ВАРИАНТ
410 М²