


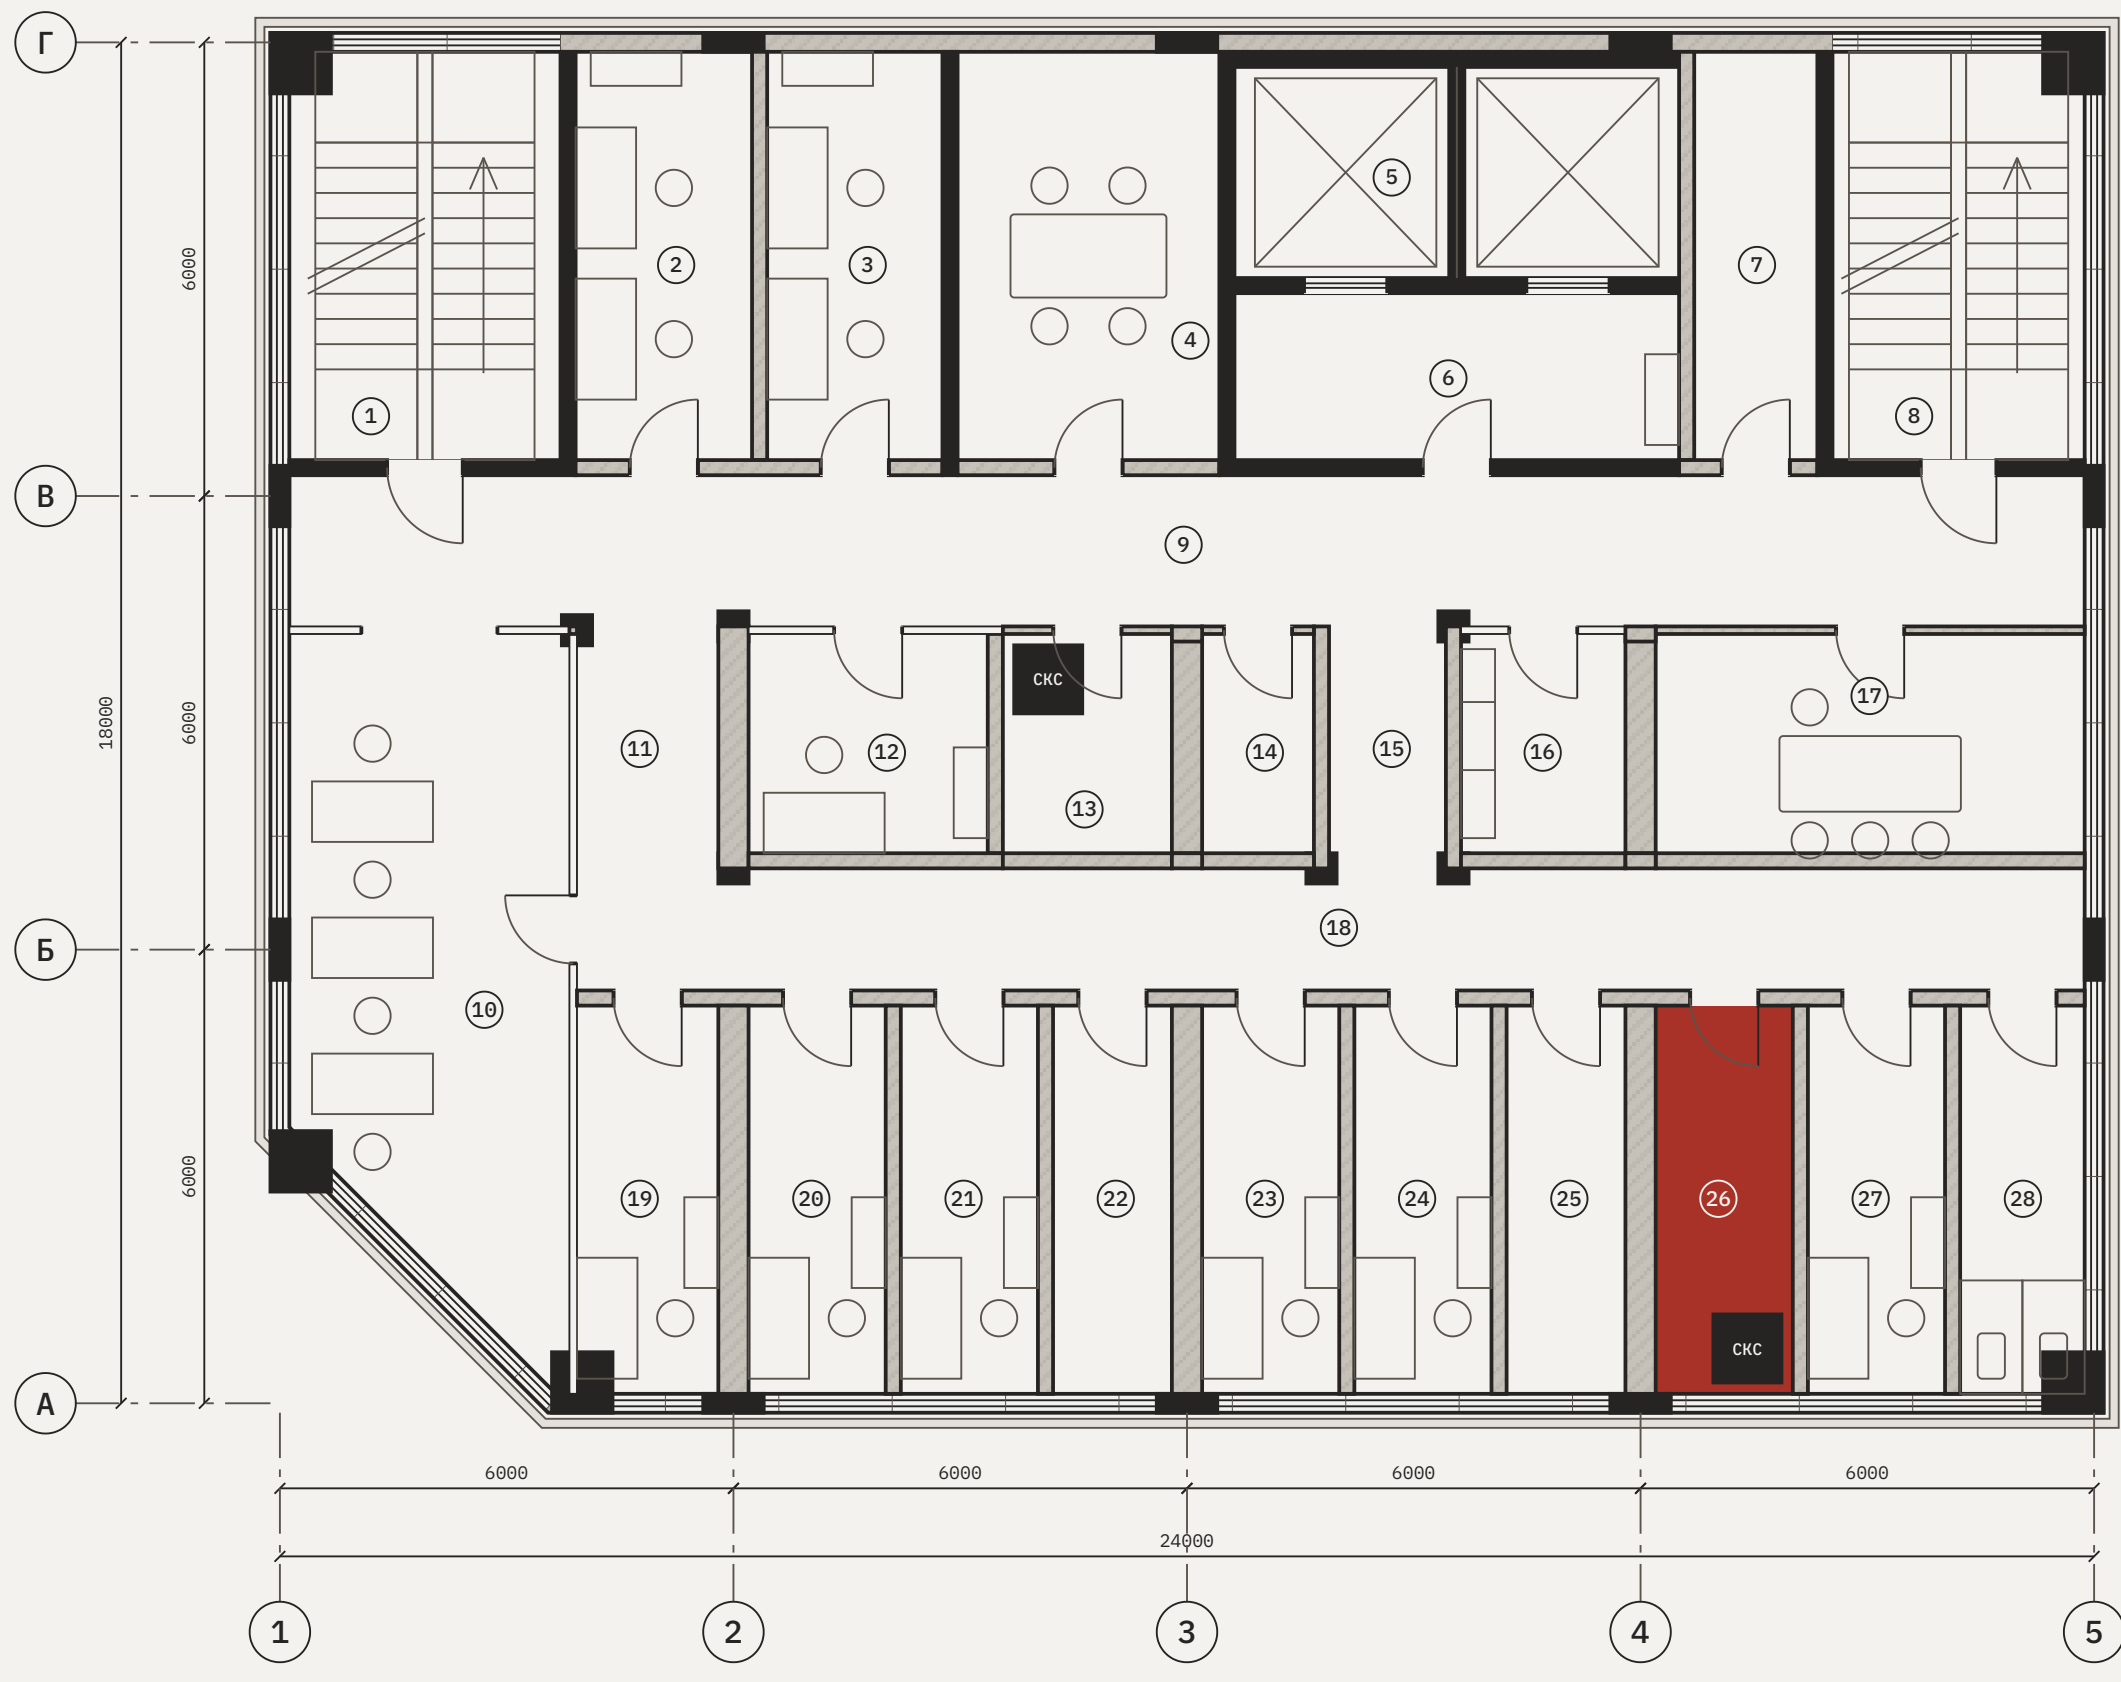

ПЛАН ЭТАЖА НА ОТМ. +0,000
М 1:100

ЭКСПЛИКАЦИЯ ПОМЕЩЕНИЙ

№	НАИМЕНОВАНИЕ	РМ	ПЛОЩАДЬ, М²
1	Лестничная клетка ЛК-1	—	19,37
2	Кабинет 4	2	12,60
3	Кабинет 1	2	12,52
4	Переговорная	—	18,70
5	Шахта на 2 лифта	—	16,42
6	Кабинет 10	1	12,99
7	Кухня-буфет	—	8,80
8	Лестничная клетка ЛК-2	—	18,01
9	Коридор главный	—	47,50
10	Опенспейс	4	31,02
11	Коридор-связь КЗ	—	5,98
12	Кабинет 9	1	9,18
13	Кроссовая СКС	—	5,67
14	Кладовая уборочного инвентаря	—	4,29
15	Коридор-связь К4	—	4,95
16	Копировальная	—	6,31
17	Переговорная малая	—	16,46
18	Коридор продольный	—	32,21
19	Кабинет 7	1	9,60
20	Кабинет 6	1	9,31
21	Кабинет 5	1	9,31
22	Электрощитовая	—	8,07
23	Кабинет 8	1	9,31
24	Кабинет 3	1	9,31
25	Тамбур-шлюз лифтового холла	—	8,07
26	Серверная	—	8,50
27	Кабинет 2	1	9,31
28	Санузел	—	8,46
ИТОГО ПОЛЕЗНАЯ		16	355,81
ПЛОЩАДЬ ЭТАЖА В ОСЯХ			425,52

УСЛОВНЫЕ ОБОЗНАЧЕНИЯ

- Пилоны, стены ядра, стояки — монолитный ж/б
- Заполнение и внутренние стены — блоки
- Перегородки светопрозрачные
- Ленточное остекление, навесной фасад
- Серверная — предмет решения листа

Красная заливка на листе несёт один смысл — серверная.
«СКС» — вертикальные стояки слаботочных сетей: связь этажа с основной и резервной серверными на других этажах. Оборудование, шкафы и кабельные трассы не показаны — они являются предметом разработки.
«РМ» — число рабочих мест в помещении.
Шахта лифтов в полезную площадь не входит.
Размеры в миллиметрах. Лист бюро, режим Б.

V71
ВАРИАНТ
426 М²