


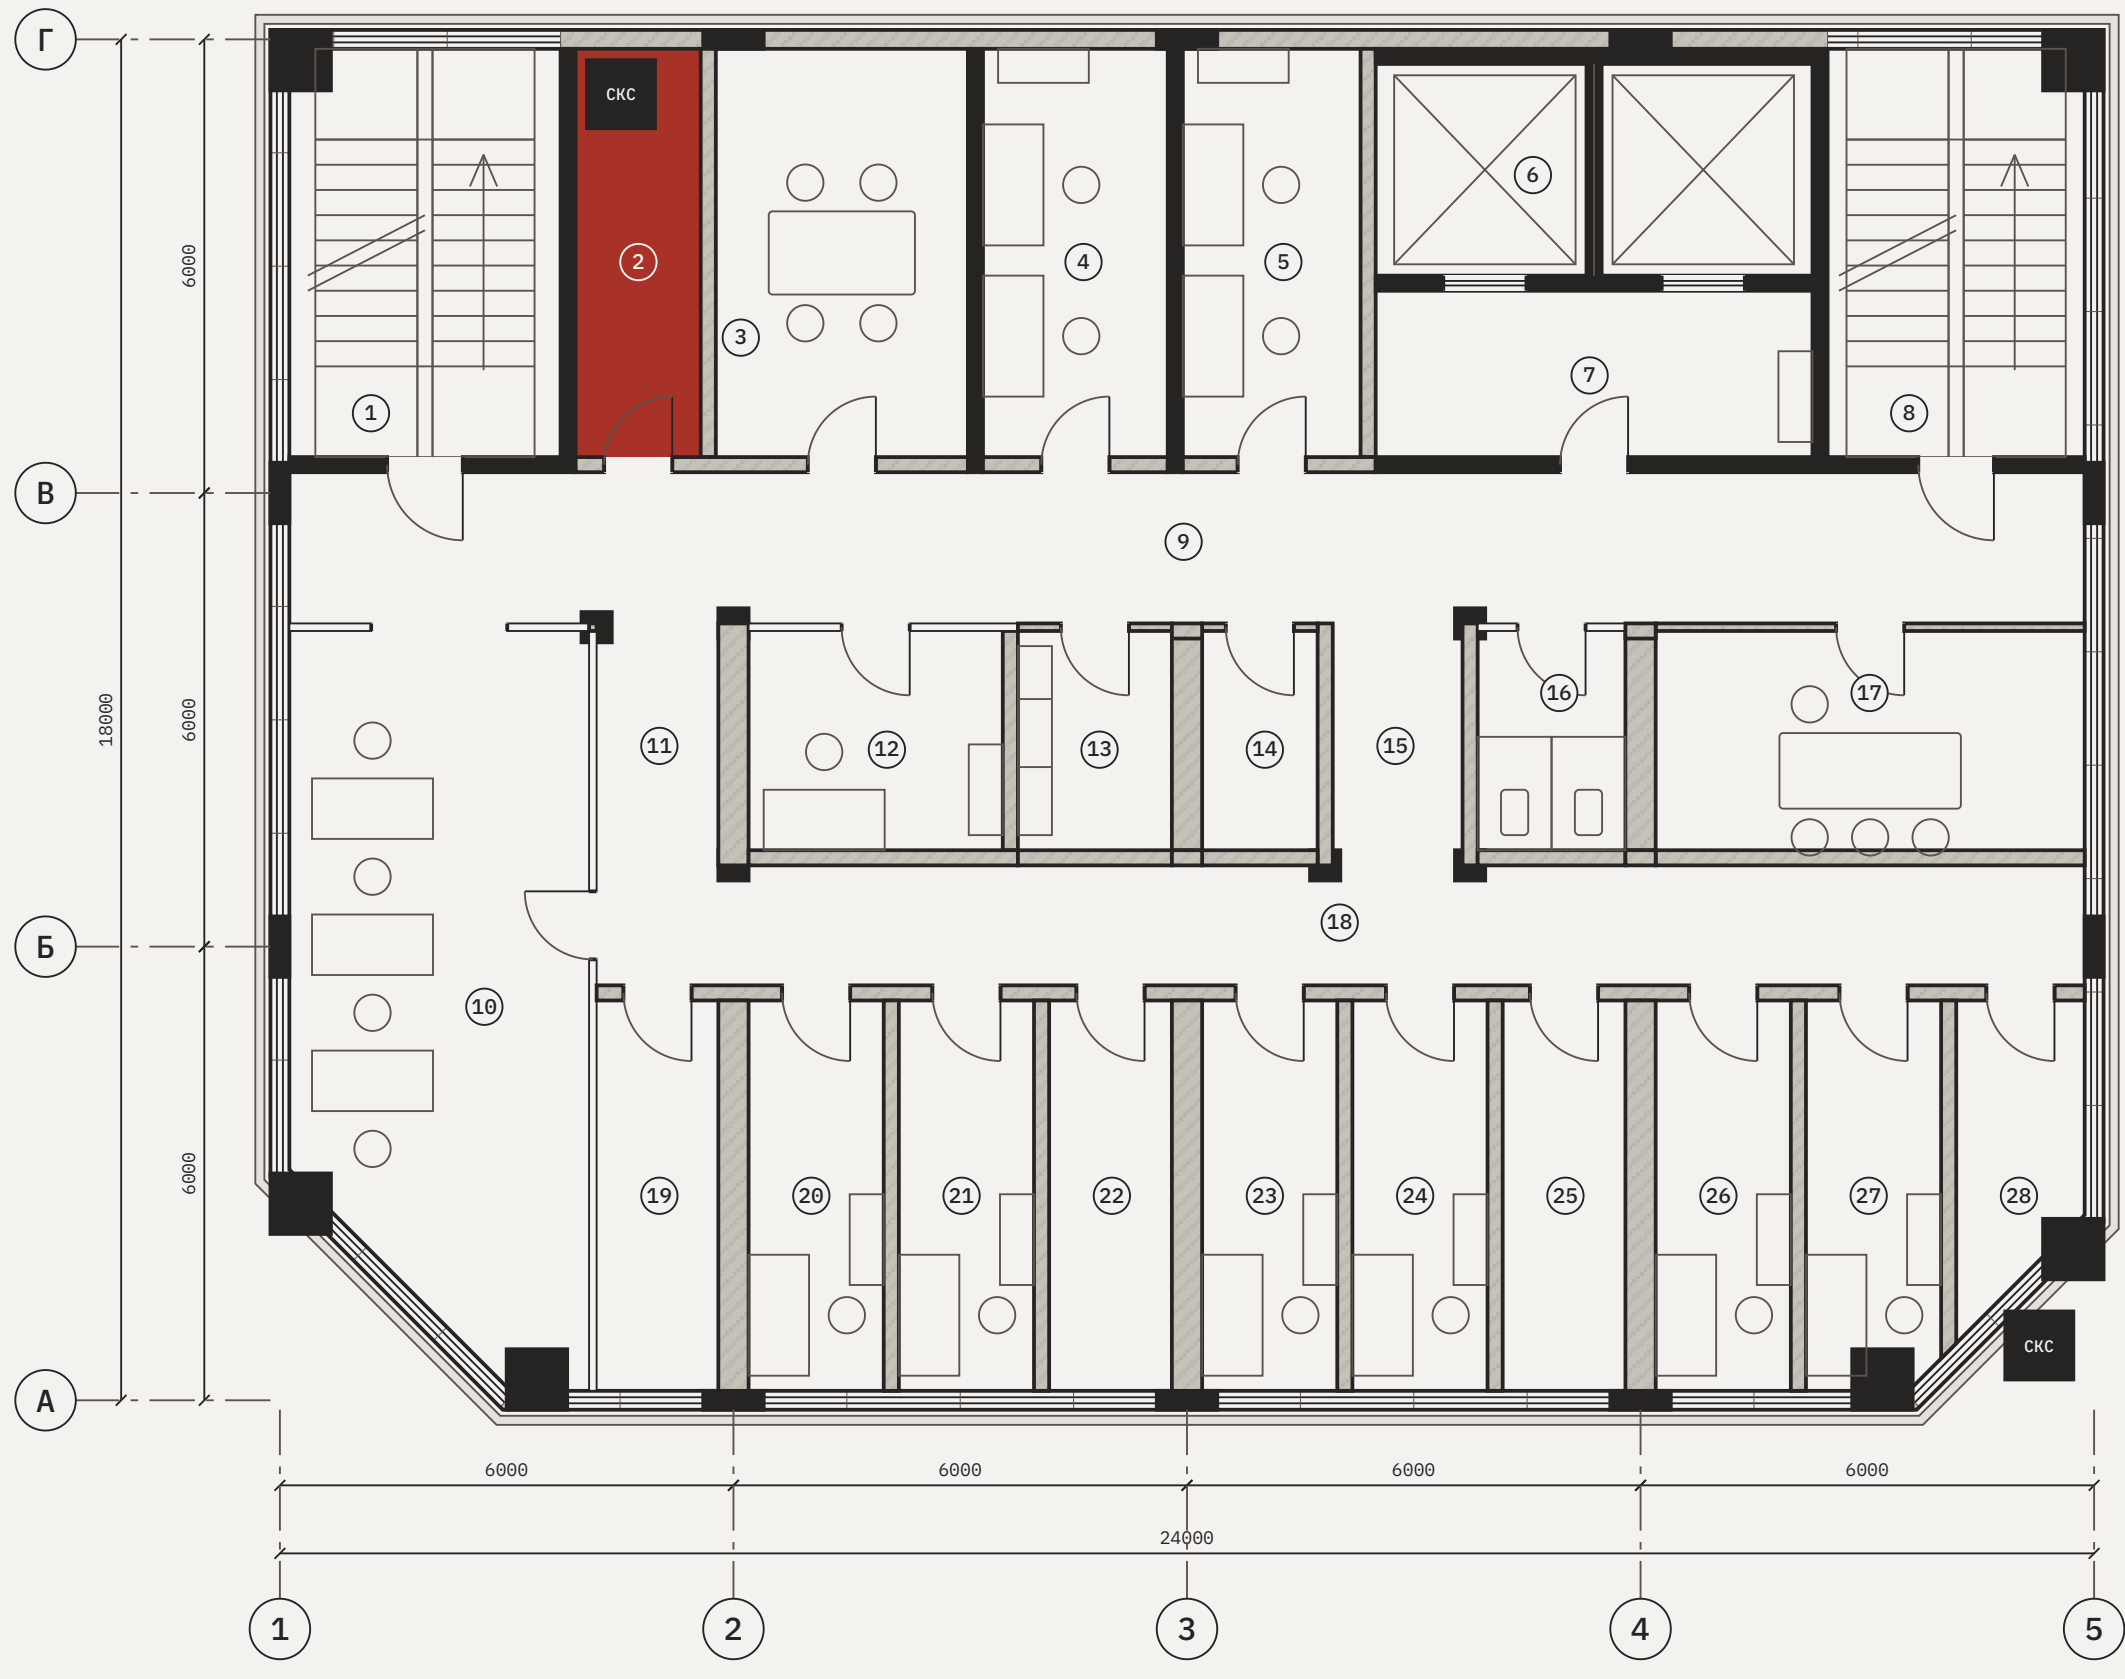

ПЛАН ЭТАЖА НА ОТМ. +0,000
М 1:100

ЭКСПЛИКАЦИЯ ПОМЕЩЕНИЙ

№	НАИМЕНОВАНИЕ	РМ	ПЛОЩАДЬ, М²
1	Лестничная клетка ЛК-1	—	19,38
2	Серверная	—	8,12
3	Переговорная	—	18,00
4	Кабинет 1	2	13,20
5	Кабинет 10	2	12,70
6	Шахта на 2 лифта	—	16,18
7	Кабинет 8	1	12,71
8	Лестничная клетка ЛК-2	—	18,37
9	Коридор главный	—	47,50
10	Опенспейс	4	35,57
11	Коридор-связь КЗ	—	5,15
12	Кабинет 4	1	9,75
13	Подсобное помещение	—	5,91
14	Электрощитовая	—	4,43
15	Коридор-связь К4	—	5,49
16	Санузел	—	5,67
17	Переговорная малая	—	16,46
18	Коридор продольный	—	31,24
19	Кухня-буфет	—	8,31
20	Кабинет 3	1	9,23
21	Кабинет 2	1	9,23
22	Тамбур-шлюз лифтового холла	—	8,38
23	Кабинет 7	1	9,23
24	Кабинет 6	1	9,23
25	Копировальная	—	8,38
26	Кабинет 5	1	9,23
27	Кабинет 9	1	9,14
28	Кроссовая СКС	—	5,45
ИТОГО ПОЛЕЗНАЯ		16	355,46
ПЛОЩАДЬ ЭТАЖА В ОСЯХ			424,62

УСЛОВНЫЕ ОБОЗНАЧЕНИЯ

- Пилоны, стены ядра, стояки — монолитный ж/б
- Заполнение и внутренние стены — блоки
- Перегородки светопрозрачные
- Ленточное остекление, навесной фасад
- Серверная — предмет решения листа

Красная заливка на листе несёт один смысл — серверная.
«СКС» — вертикальные стояки слаботочных сетей: связь этажа с основной и резервной серверными на других этажах. Оборудование, шкафы и кабельные трассы не показаны — они являются предметом разработки.
«РМ» — число рабочих мест в помещении.
Шахта лифтов в полезную площадь не входит.
Размеры в миллиметрах. Лист бюро, режим Б.

V79
ВАРИАНТ
425 М²